



СТРОПИЛЬНАЯ СИСТЕМА КРОВЛИ				
№	НАЗНАЧЕНИЕ	РАЗМЕР, ММ	КОЛ-ВО ШТ.	ПРИМЕЧАНИЕ
1	СТРОПИЛЬНАЯ НОГА	4400x50x150	4	V=0.133 м³
2	СТРОПИЛЬНАЯ НОГА	3700x50x150	4	V=0.108 м³
3	СТРОПИЛЬНАЯ НОГА	2900x50x150	4	V=0.084 м³
4	СТРОПИЛЬНАЯ НОГА	2200x50x150	4	V=0.064 м³
5	СТРОПИЛЬНАЯ НОГА	1500x50x150	4	V=0.044 м³
6	СТРОПИЛЬНАЯ НОГА	750x50x150	1	V=0.0056 м³
7	СТРОПИЛЬНАЯ НОГА	1400x50x150	2	V=0.042 м³
8	СТРОПИЛЬНАЯ НОГА	4200x50x150	2	V=0.063 м³
9	СТРОПИЛЬНАЯ НОГА	1900x50x150	2	V=0.0028 м³
10	СТРОПИЛЬНАЯ НОГА	1300x50x150	2	V=0.00195 м³
11	СТРОПИЛЬНАЯ НОГА	700x50x150	2	V=0.0105 м³
12	СТРОПИЛЬНАЯ НОГА	600x50x150	2	V=0.009 м³
13	СТРОПИЛЬНАЯ НОГА	1400x50x150	2	V=0.021 м³
14	СТРОПИЛЬНАЯ НОГА	2300x50x150	1	V=0.0172 м³
15	СТРОПИЛЬНАЯ НОГА	3000x50x150	1	V=0.0225 м³
16	СТРОПИЛЬНАЯ НОГА	990x50x150	2	V=0.0148 м³
17	СТРОПИЛЬНАЯ НОГА	2200x50x150	2	V=0.0033 м³
18	СТРОПИЛЬНАЯ НОГА	2700x50x150	4	V=0.081 м³
19	СТРОПИЛЬНАЯ НОГА	1100x50x150	2	V=0.0165 м³
20	СТРОПИЛЬНАЯ НОГА	900x50x150	1	V=0.0067 м³
21	СТРОПИЛЬНАЯ НОГА	730x50x150	2	V=0.0109 м³
22	СТРОПИЛЬНАЯ НОГА	500x50x150	2	V=0.0075 м³
23	СТРОПИЛЬНАЯ НОГА	300x50x150	2	V=0.0045 м³
24	СТРОПИЛЬНАЯ НОГА	500x50x150	4	V=0.015 м³
25	СТРОПИЛЬНАЯ НОГА	1200x50x150	4	V=0.036 м³
26	СТРОПИЛЬНАЯ НОГА	1800x50x150	4	V=0.054 м³
27	СТРОПИЛЬНАЯ НОГА	2500x50x150	4	V=0.075 м³
28	СТРОПИЛЬНАЯ НОГА	3100x50x150	4	V=0.093 м³
29	СТРОПИЛЬНАЯ НОГА	4000x50x150	2	V=0.06 м³
30	СТРОПИЛЬНАЯ НОГА	6900x50x150	4	V=0.207 м³
31	МАУЗЕРЛАТ	9200x100x100	4	V=0.37 м³
32	КОНЕК 1	1300x50x150	1	V=0.0097 м³
33	КОБЫЛКА 1	1000x50x150	48	V=0.36 м³
34	ЕНДОВА 1	6900x50x150	4	V=0.207 м³
35	КОБЫЛКА 2	500x50x150	13	V=0.0048 м³
36	ЕНДОВА 2	4200x50x150	2	V=0.063 м³
37	КОНЕК	915x50x150	1	V=0.0068 м³
38	КОБЫЛКА 3	300x50x150	5	V=0.0125 м³
39	ЕНДОВА 3	2800x50x150	2	V=0.042 м³
40	ОБРЕШ. ДОСКА	900x40x100	2	V=0.0072 м³
41	ОБРЕШ. ДОСКА	2600x40x100	2	V=0.0208 м³
42	ОБРЕШ. ДОСКА	3500x40x100	2	V=0.028 м³
43	ОБРЕШ. ДОСКА	4800x40x100	2	V=0.0384 м³
44	ОБРЕШ. ДОСКА	6100x40x100	2	V=0.0488 м³
45	ОБРЕШ. ДОСКА	7300x40x100	2	V=0.0584 м³
46	ОБРЕШ. ДОСКА	8650x40x100	2	V=0.0692 м³
47	ОБРЕШ. ДОСКА	1700x40x100	2	V=0.0136 м³
48	ОБРЕШ. ДОСКА	2900x40x100	2	V=0.0232 м³
49	ОБРЕШ. ДОСКА	4000x40x100	2	V=0.032 м³
50	ОБРЕШ. ДОСКА	5100x40x100	2	V=0.0408 м³
51	ОБРЕШ. ДОСКА	6300x40x100	2	V=0.0504 м³
52	ОБРЕШ. ДОСКА	7400x40x100	2	V=0.0592 м³
53	ОБРЕШ. ДОСКА	8500x40x100	2	V=0.068 м³
54	ОБРЕШ. ДОСКА	9600x40x100	2	V=0.0768 м³

ПЛАН ДЕРЕВЯННЫХ ПЕРЕКРЫТИЙ

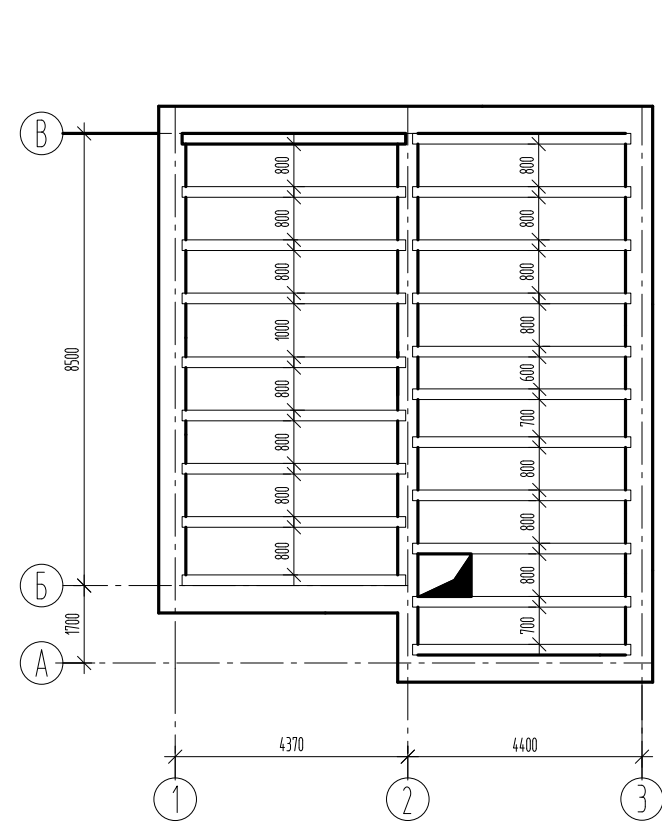

ПЛАН ФУНДАМЕНТА

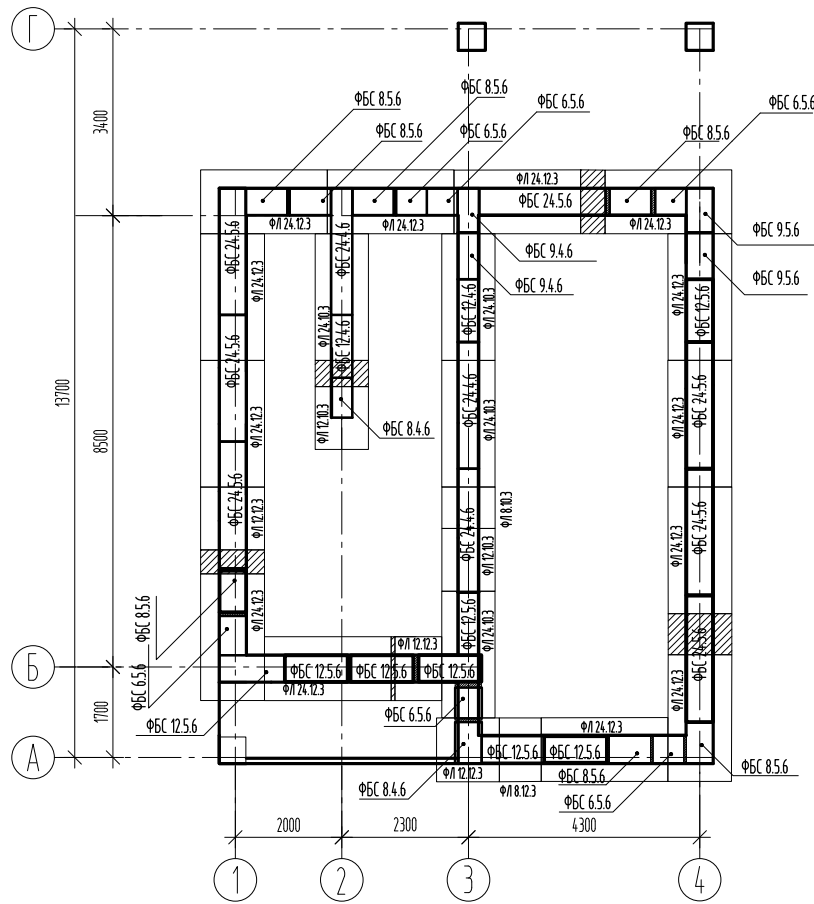


ВЕДОМОСТЬ ДЕРЕВЯННЫХ ПЕКРЕТЫЙ			
№	РАЗМЕР	КОЛ-ВО	ПРИМЕЧАНИЕ
1	4100x150x100	11	V=0.68 м³
2	4200x150x100	9	V=0.57 м³


ВЕДОМОСТЬ ПЕРЕМЫЧЕК М150

ОБОЗНАЧ.	ЭСКИЗ	ШИРИНА ПРОЕМА	СОСТАВ НА ОДНО МЕСТО	ОБЩЕЕ КОЛИЧЕСТВО	
ПБ 1 (3 ШТ.)		2500	ЗПБ-30-3П (1 ШТ) 2ПБ-30-3П (3 ШТ)	3 ШТ.	9 ШТ.
ПБ 2 (2 ШТ.)		2400	ЗПБ-29-3П (1 ШТ) 2ПБ-29-3П (3 ШТ)	2 ШТ.	6 ШТ.
ПБ 4 (1 ШТ.)		3100	ЗПБ-36-8П (1 ШТ) 2ПБ-36-3П (3 ШТ)	1 ШТ.	3 ШТ.
ПБ 5 (3 ШТ.)		1500	ЗПБ-20-4П (1 ШТ) 2ПБ-20-4П (3 ШТ)	3 ШТ.	9 ШТ.
ПБ 3 (3 ШТ.)		2400	2ПБ-28-8П (4 ШТ)	12 ШТ.	
ПБ 6 (3 ШТ.)		900	2ПБ-13-П (1 ШТ)	3 ШТ.	
ПБ 9 (2 ШТ.)		700	2ПБ-10-П (1 ШТ)	2 ШТ.	
МУ 1 МЕСТ. 1		1510	0,12x1510=0,1812	1 ШТ.	


ПЛАН ПЕРЕМЫЧЕК 1 ЭТАЖА

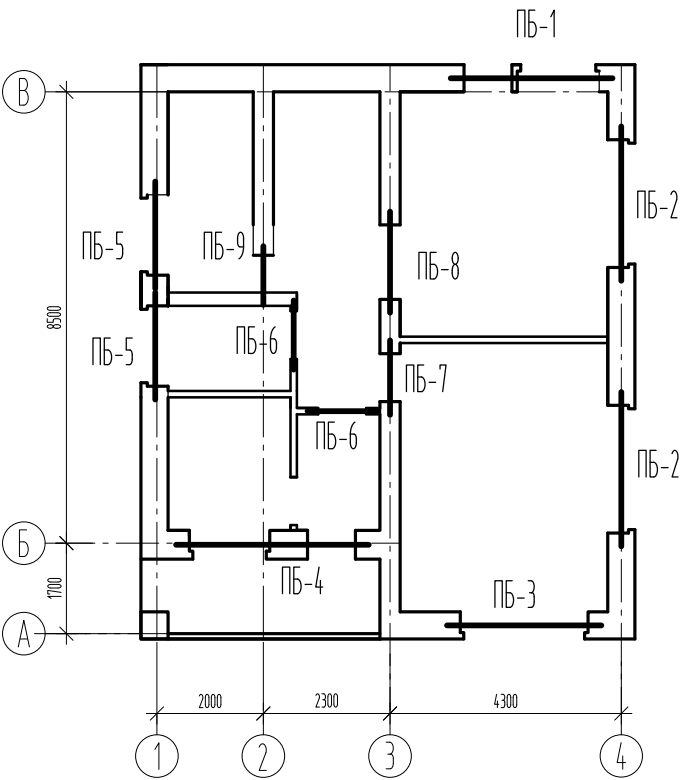

ПЛАН ПЕРЕМЫЧЕК 2 ЭТАЖА

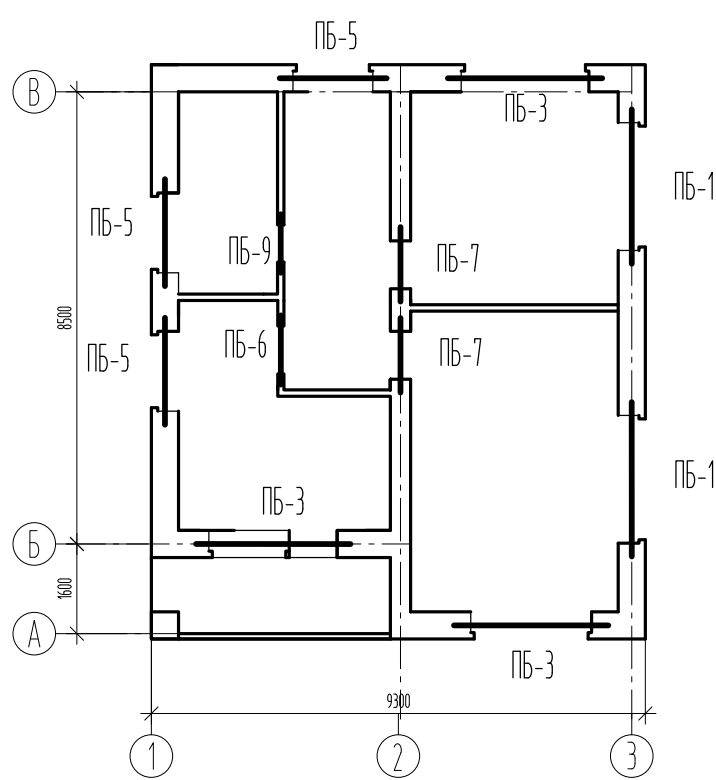

ПЛАН ПЕРЕКРЫТИЙ

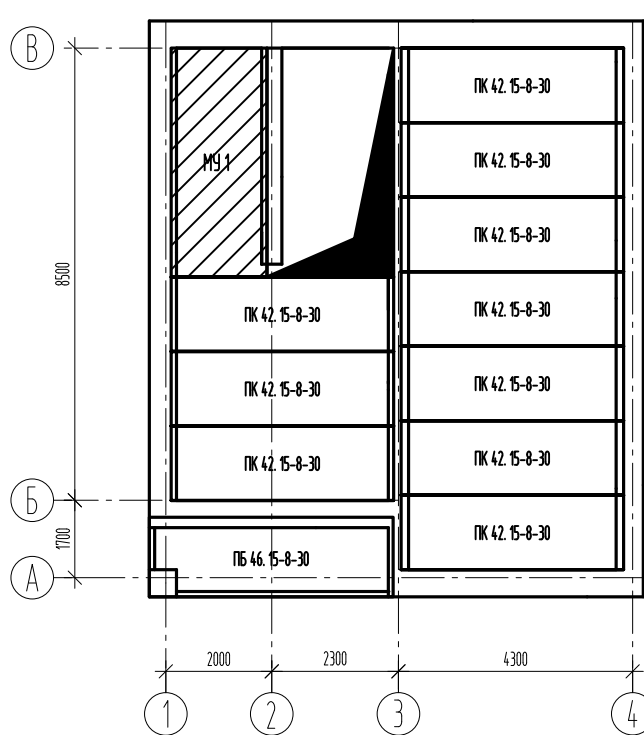

ВЕДОМОСТЬ СБОРНОГО ФУНДАМЕНТА		
№ ПОИ	НАИМЕНОВАНИЕ БЛОКА	КОЛ-ВО
1	ФБС 24.5.6	7
2	ФБС 12.5.6	7
3	ФБС 9.5.6	2
4	ФБС 8.5.6	8
5	ФБС 6.5.6	6
6	ФБС 24.4.6	3
7	ФБС 12.4.6	3
8	ФБС 9.4.6	2
9	ФБС 8.4.6	1
10	ФЛ 24.12.3	13
11	ФЛ 12.12.3	3
12	ФЛ 8.12.3	1
13	ФЛ 24.10.3	4
14	ФЛ 12.10.3	2
15	ФЛ 8.10.3	1

ЭКСПЛИКАЦИЯ ПЛИТ ПЕРЕКРЫТИЙ		
НАИМЕНОВАНИЕ	РАЗМЕР	КОЛ-ВО
ПК 42. 15-8-30	4800x495x220	10
ПБ 46. 15-8-60	4580x495x220	1
МУ 1	4300x1800x220	1

				ГБПОУ КАС 7 08.02.01 КП		
				КОНСТРУКТИВНАЯ ЧАСТЬ		
ДОЛЖНОСТЬ	ФАМИЛИЯ	ПОДПИСЬ	ДАТА	ДВУХЭТАЖНЫЙ КОТТЕДЖ		
				СТАДИЯ	ЛИСТ	ЛИСТОВ
				У	2	2
РУКОВОДИТ.	ЖИГУНЕНКО И.В.	ПЛАН ПЛИТ ПЕРЕКРЫТИЙ 1-ГО ЭТАЖА, ПЛАН ДЕРЕВЯННЫХ ПЕРЕКРЫТИЙ, ПЛАН ФУНДАМЕНТА, ПЛАН СТРОПИЛ, ПЛАН ПЕРЕМЫЧЕК 1-ГО И 2-ГО И ЦОКОЛЬНОГО ЭТАЖА				
КОНСУЛЬТ.	ВОЛКОВА Н.В.					
ВЫПОЛНИЛ	ГЛАЖКОВА М.А.					
				ПД-31 2023 г.		