




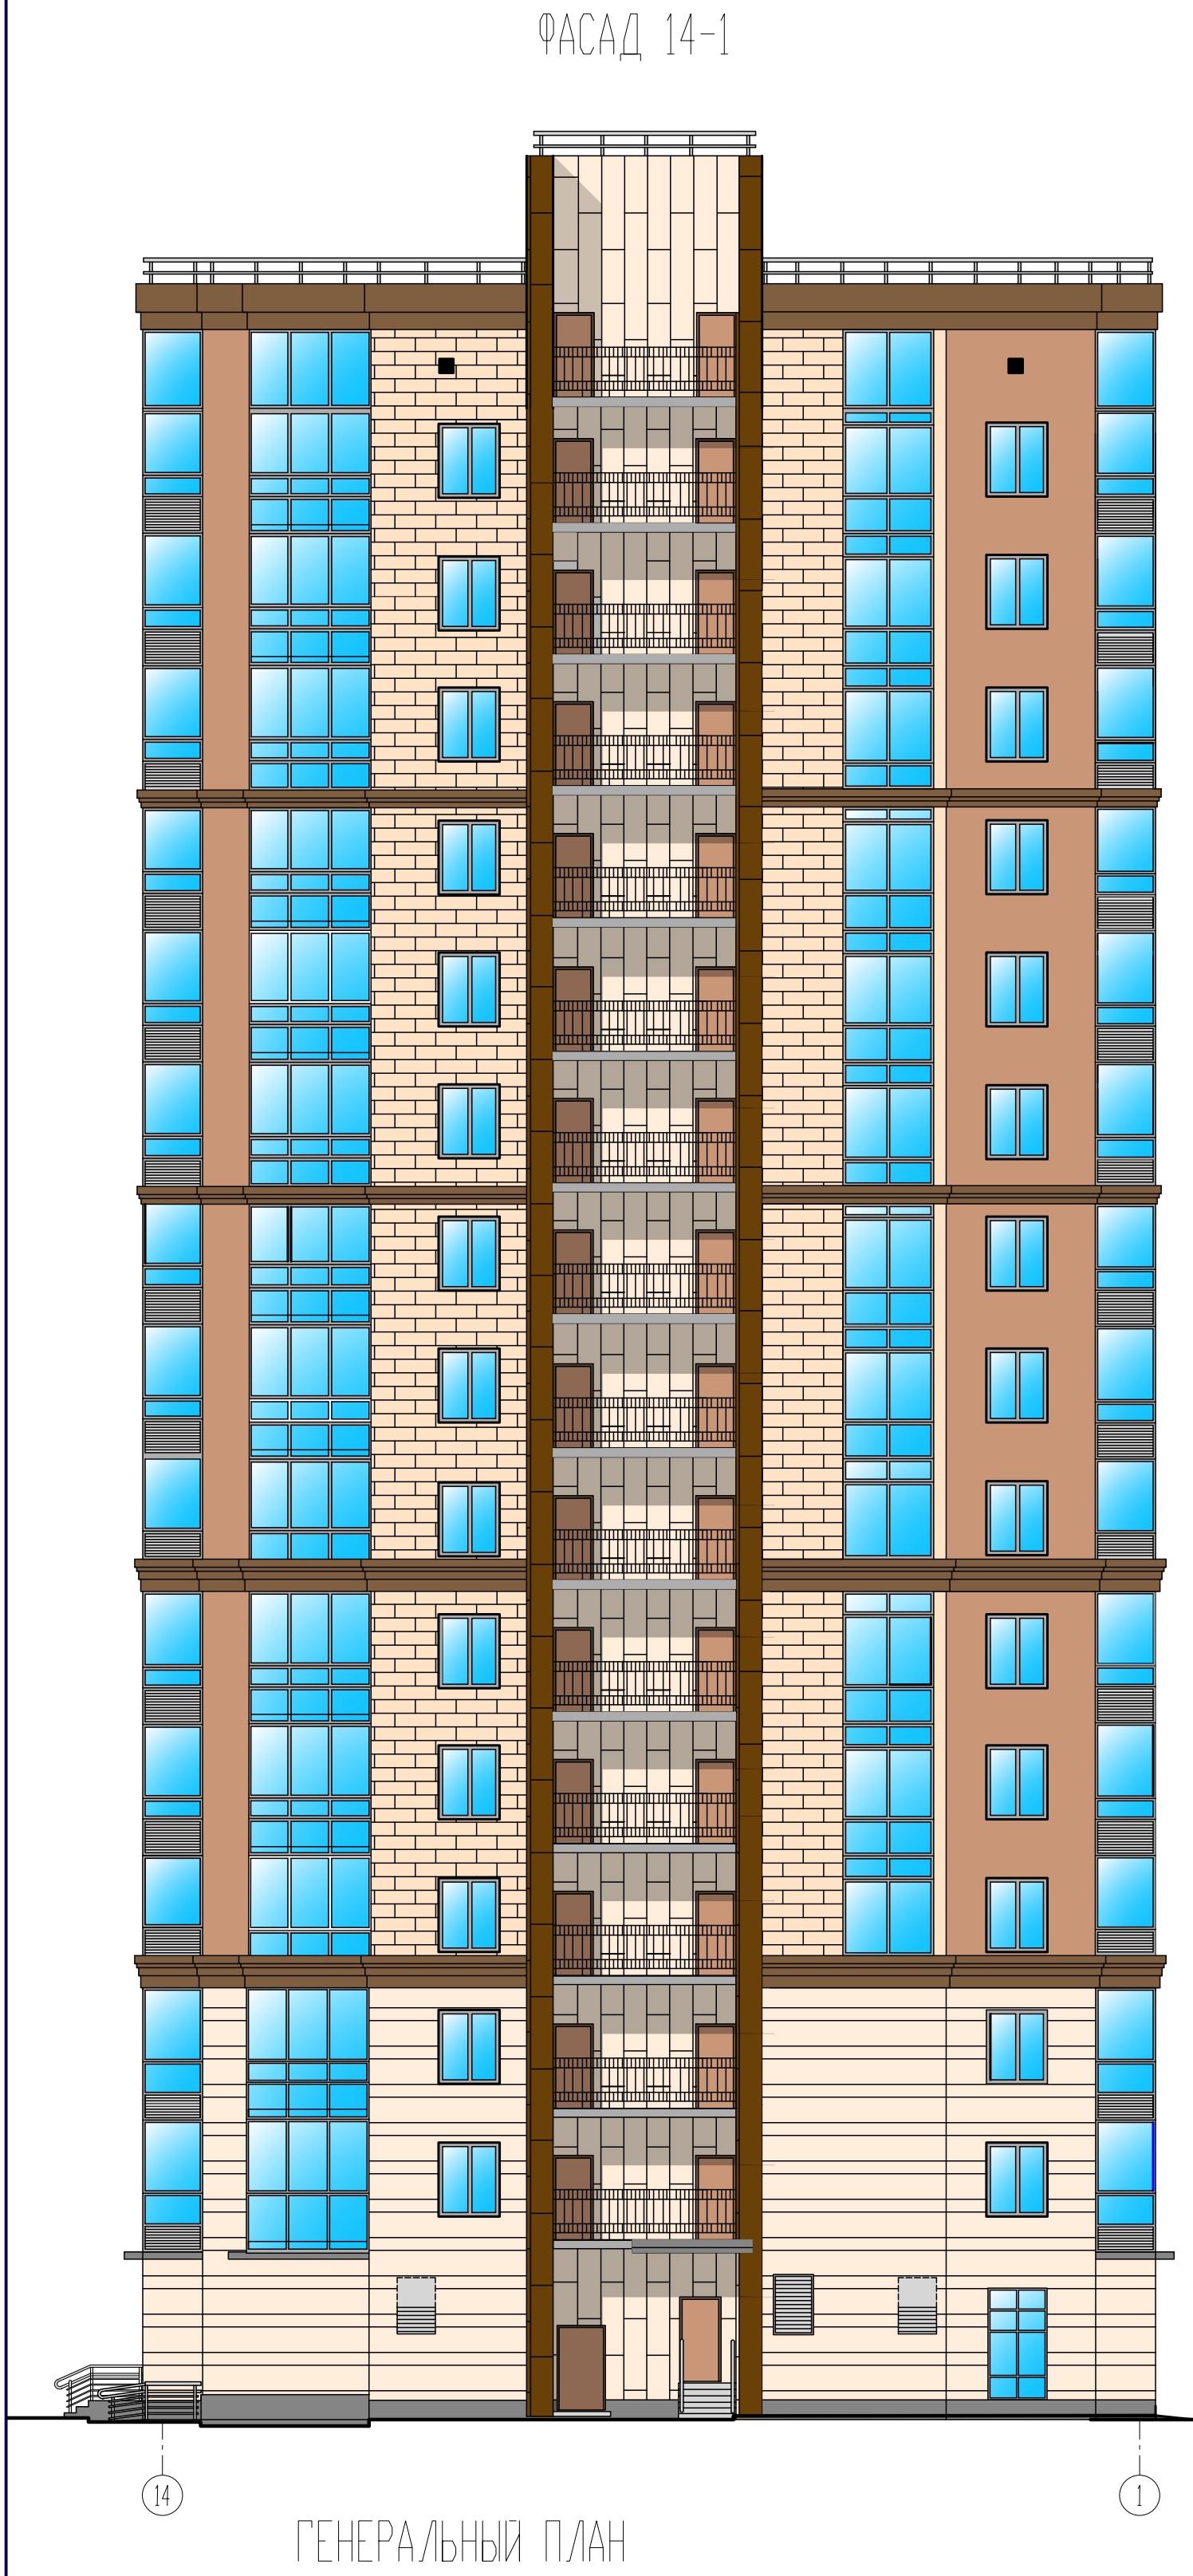


УСЛОВНЫЕ ОБОЗНАЧЕНИЯ	
? П/П	ОБОЗНАЧЕНИЕ
1	ДЕРЕВО
2	КУСТАРНИК
3	ПАРКОВАННОЕ МЕСТО
4	ЭЛЕМЕНТЫ ДЕТСКОЙ ПЛОЩАДКИ
5	ЛАВЧКА
6	ПЛОЩАДКА ДЛЯ МЫСОРА
7	ТРАССА
8	АВТОМОБИЛЬНЫЕ ДОРОЖКИ
9	ПЕШЕХОДНЫЕ ДОРОЖКИ
10	РЕЗИНОВЫЕ ПОКРЫТИЕ

ЭКСПЛИКАЦИЯ ГЕНЕРАЛЬНОГО ПЛАНА	
? П/П	НАИМЕНОВАНИЕ
1	ПРОЕКТИРУЕМЫЙ ДОМ
2	ДЕТСКАЯ ПЛОЩАДКА
3	КРЫТАЯ ПАРКОВКА
4	ПАРКОВКА
5	МЕСТО ДЛЯ ОТДЫХА

ЭКСПЛИКАЦИЯ ОКОН			
ОКНА	РАЗМЕР	КОЛ-ВО НА 1 ЭТАЖ	КОЛ-ВО НА ТИПОВОМ ЭТАЖ
ОК 1	1840 x 1530	3	2
ОК 2 бал.	1430 x 800	3	4
ОК 3	1840 x 1170	1	1

ЭКСПЛИКАЦИЯ ДВЕРЕЙ				
ДВЕРИ	РАЗМЕР	КОЛ-ВО НА 1 ЭТАЖ	КОЛ-ВО НА ТИПОВОМ ЭТАЖ	КОЛ-ВО НА ПОДВАЛ
Д1	2100 x 1300	8	2	-
Д2	2100 x 1200	-	1	-
Д3	2100 x 1100	9	2	-
Д4	2100 x 1000	2	8	5
Д5	2100 x 800	-	9	-
Д6	2100 x 700	-	7	3
Д7	2100 x 600	8	15	-

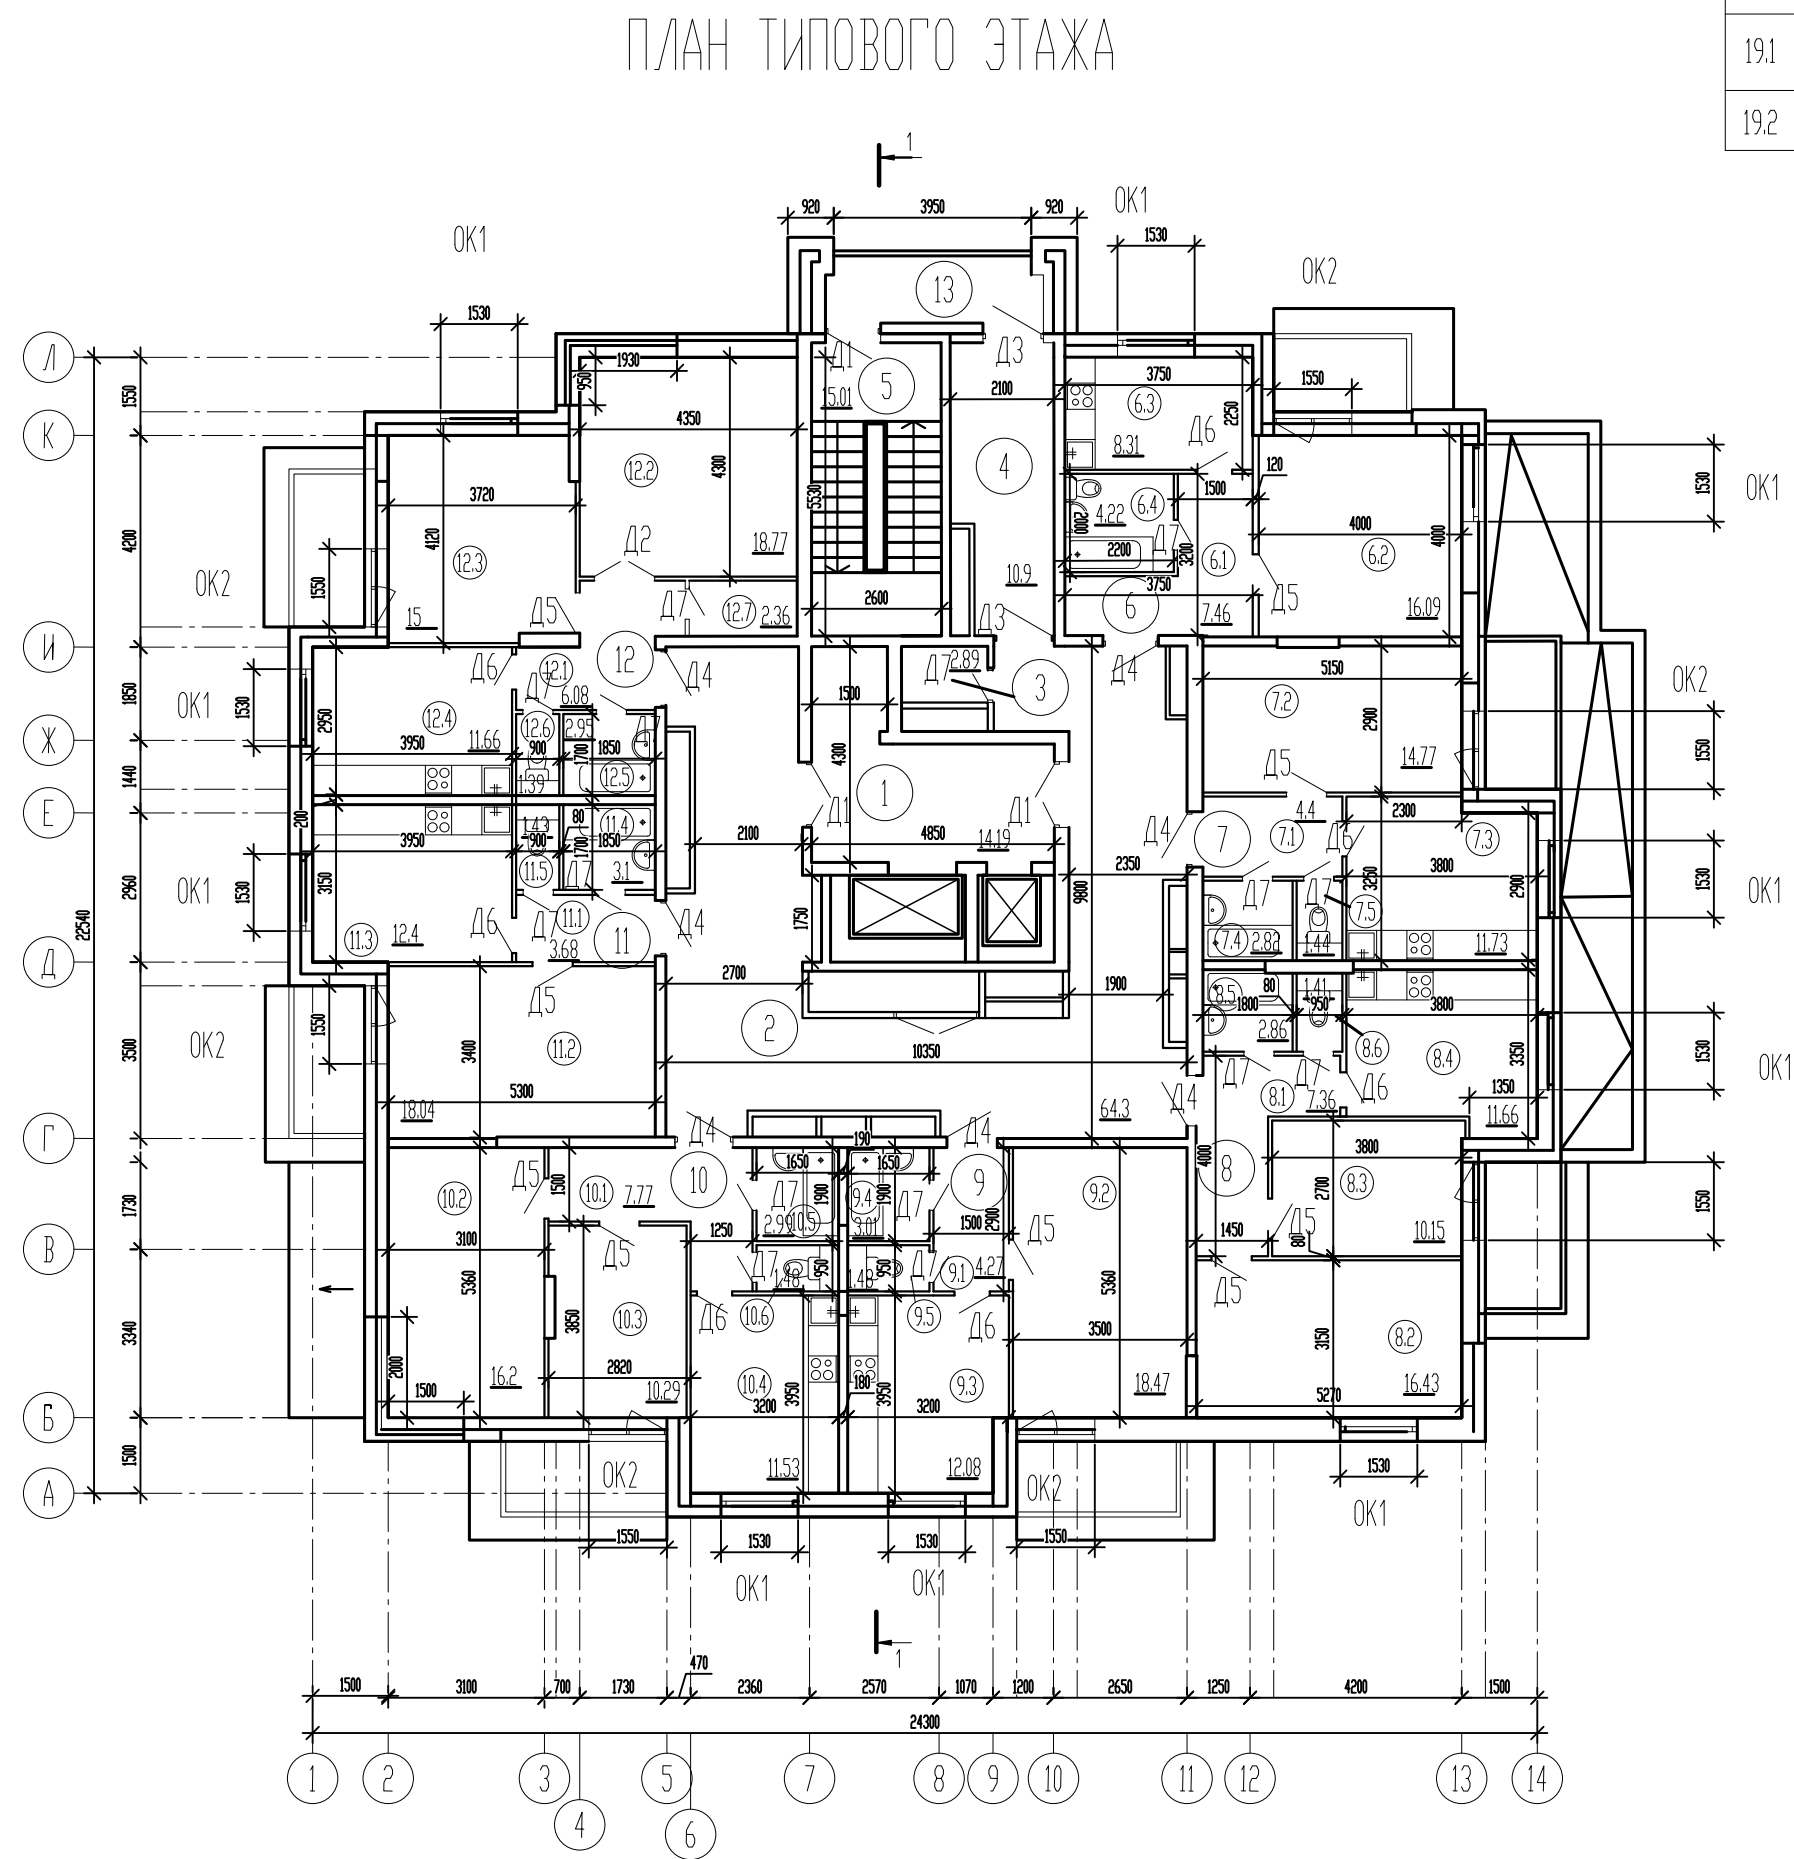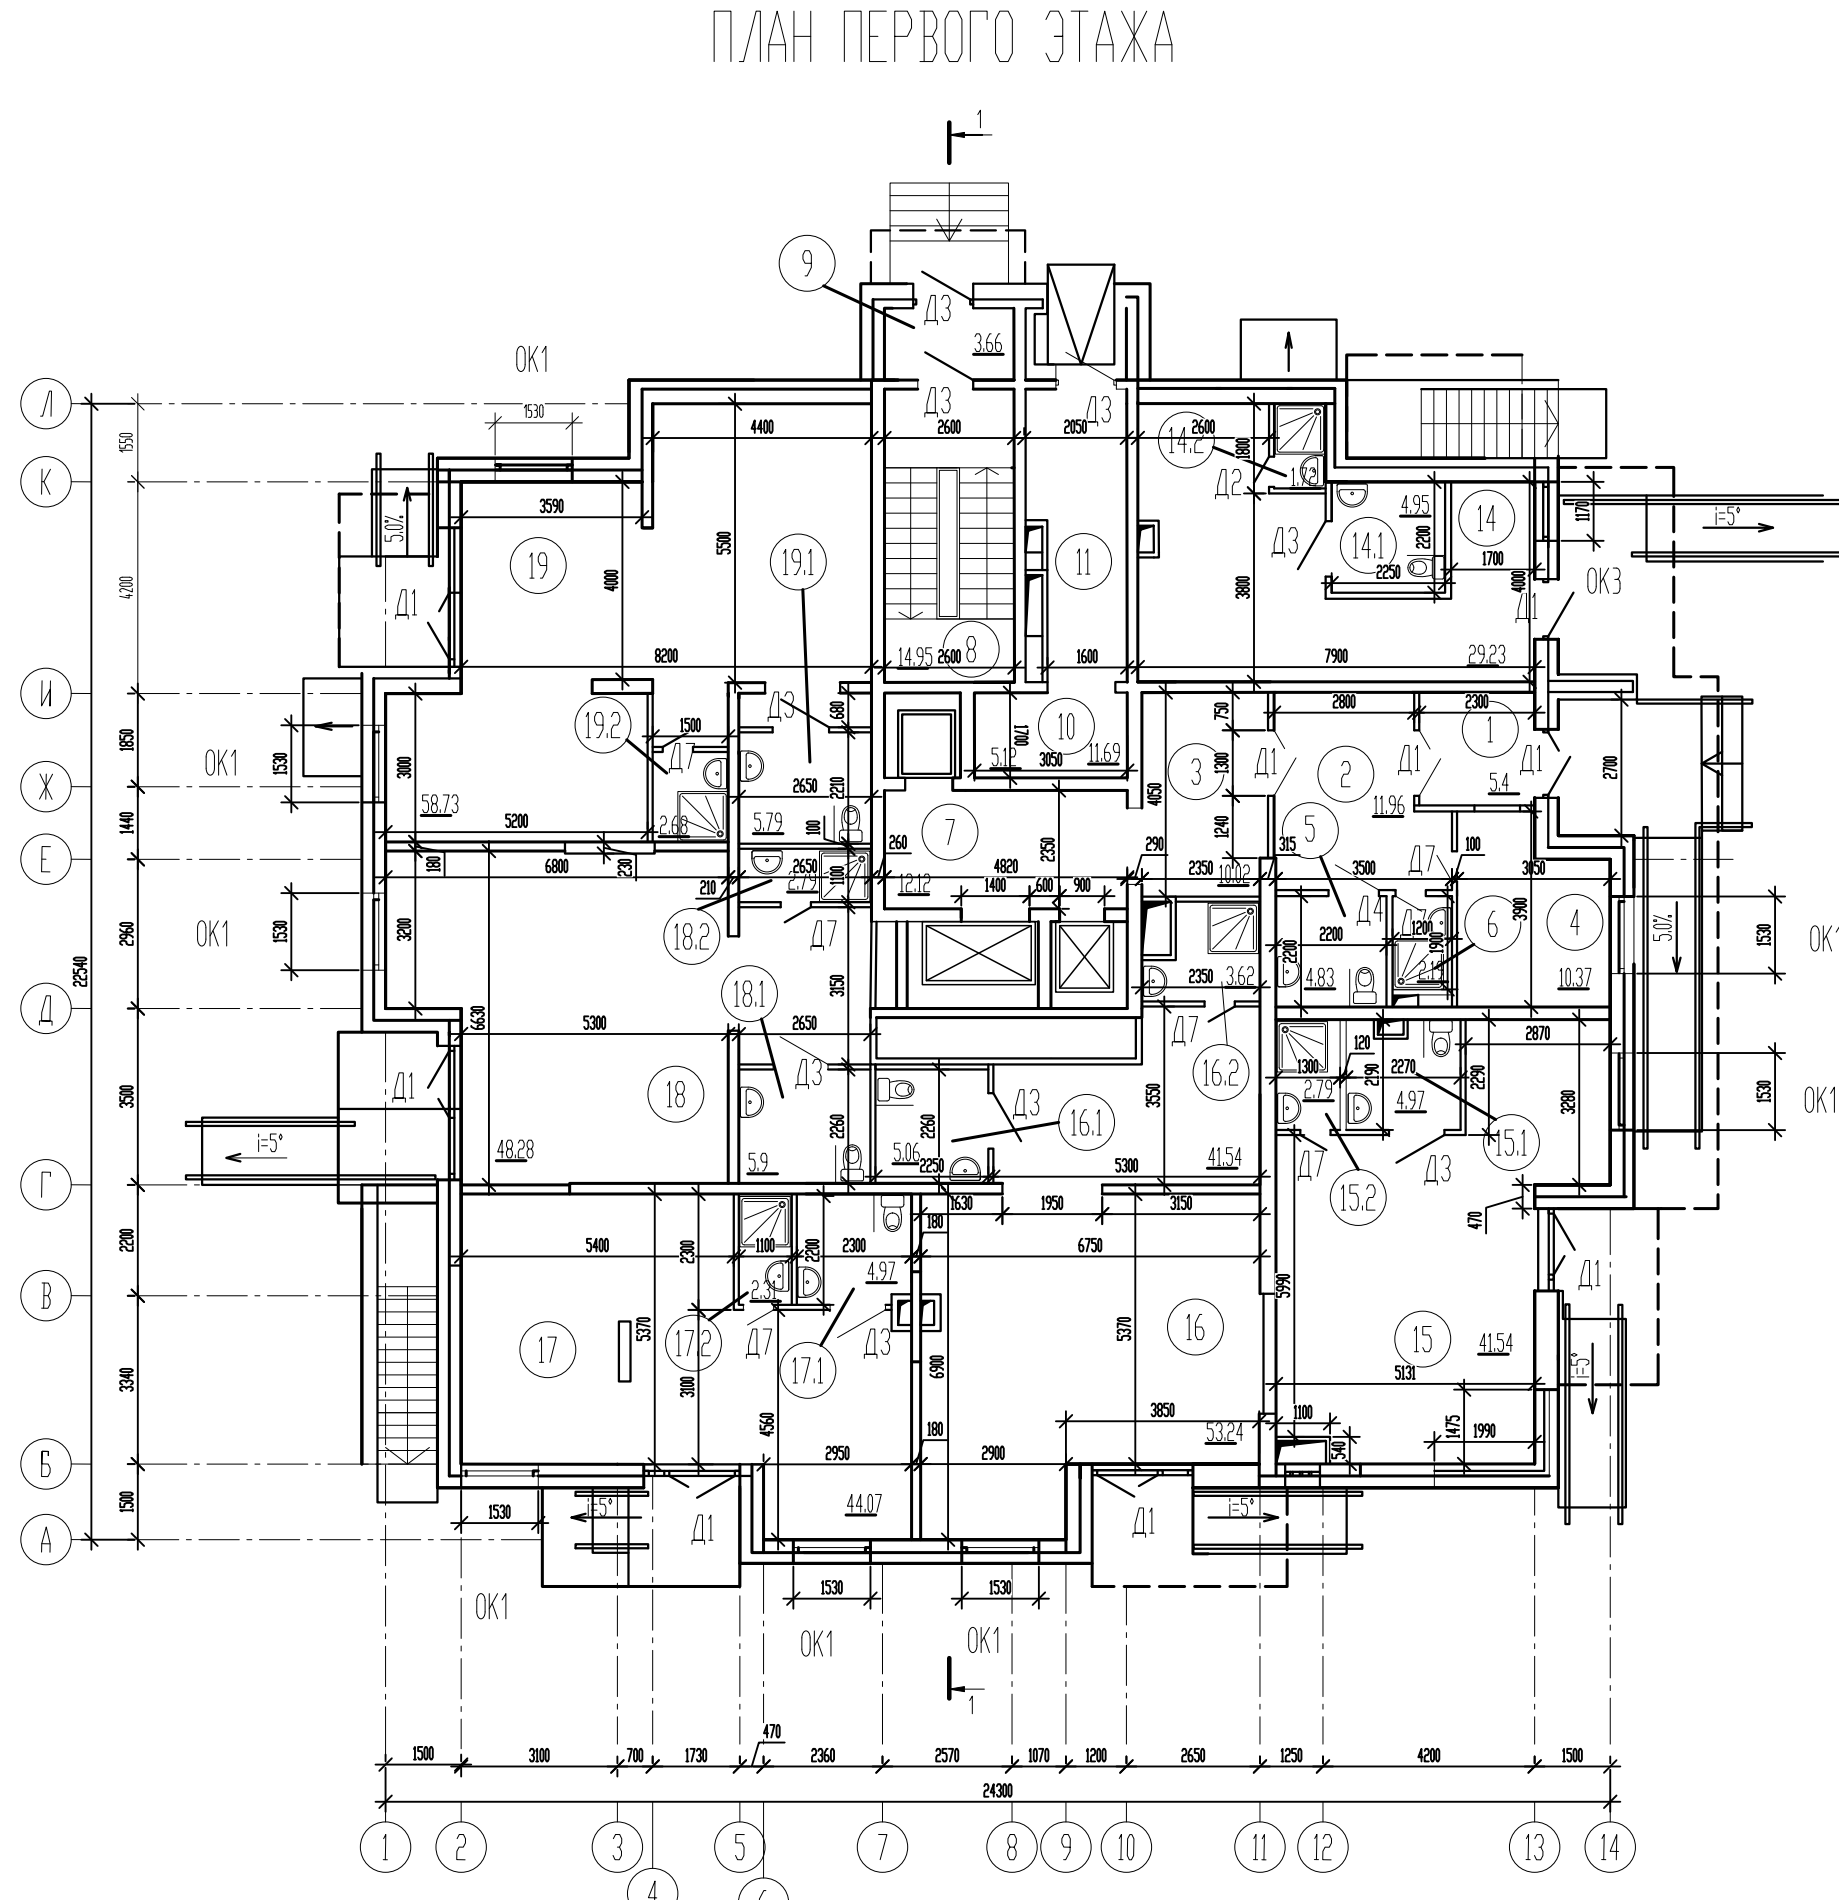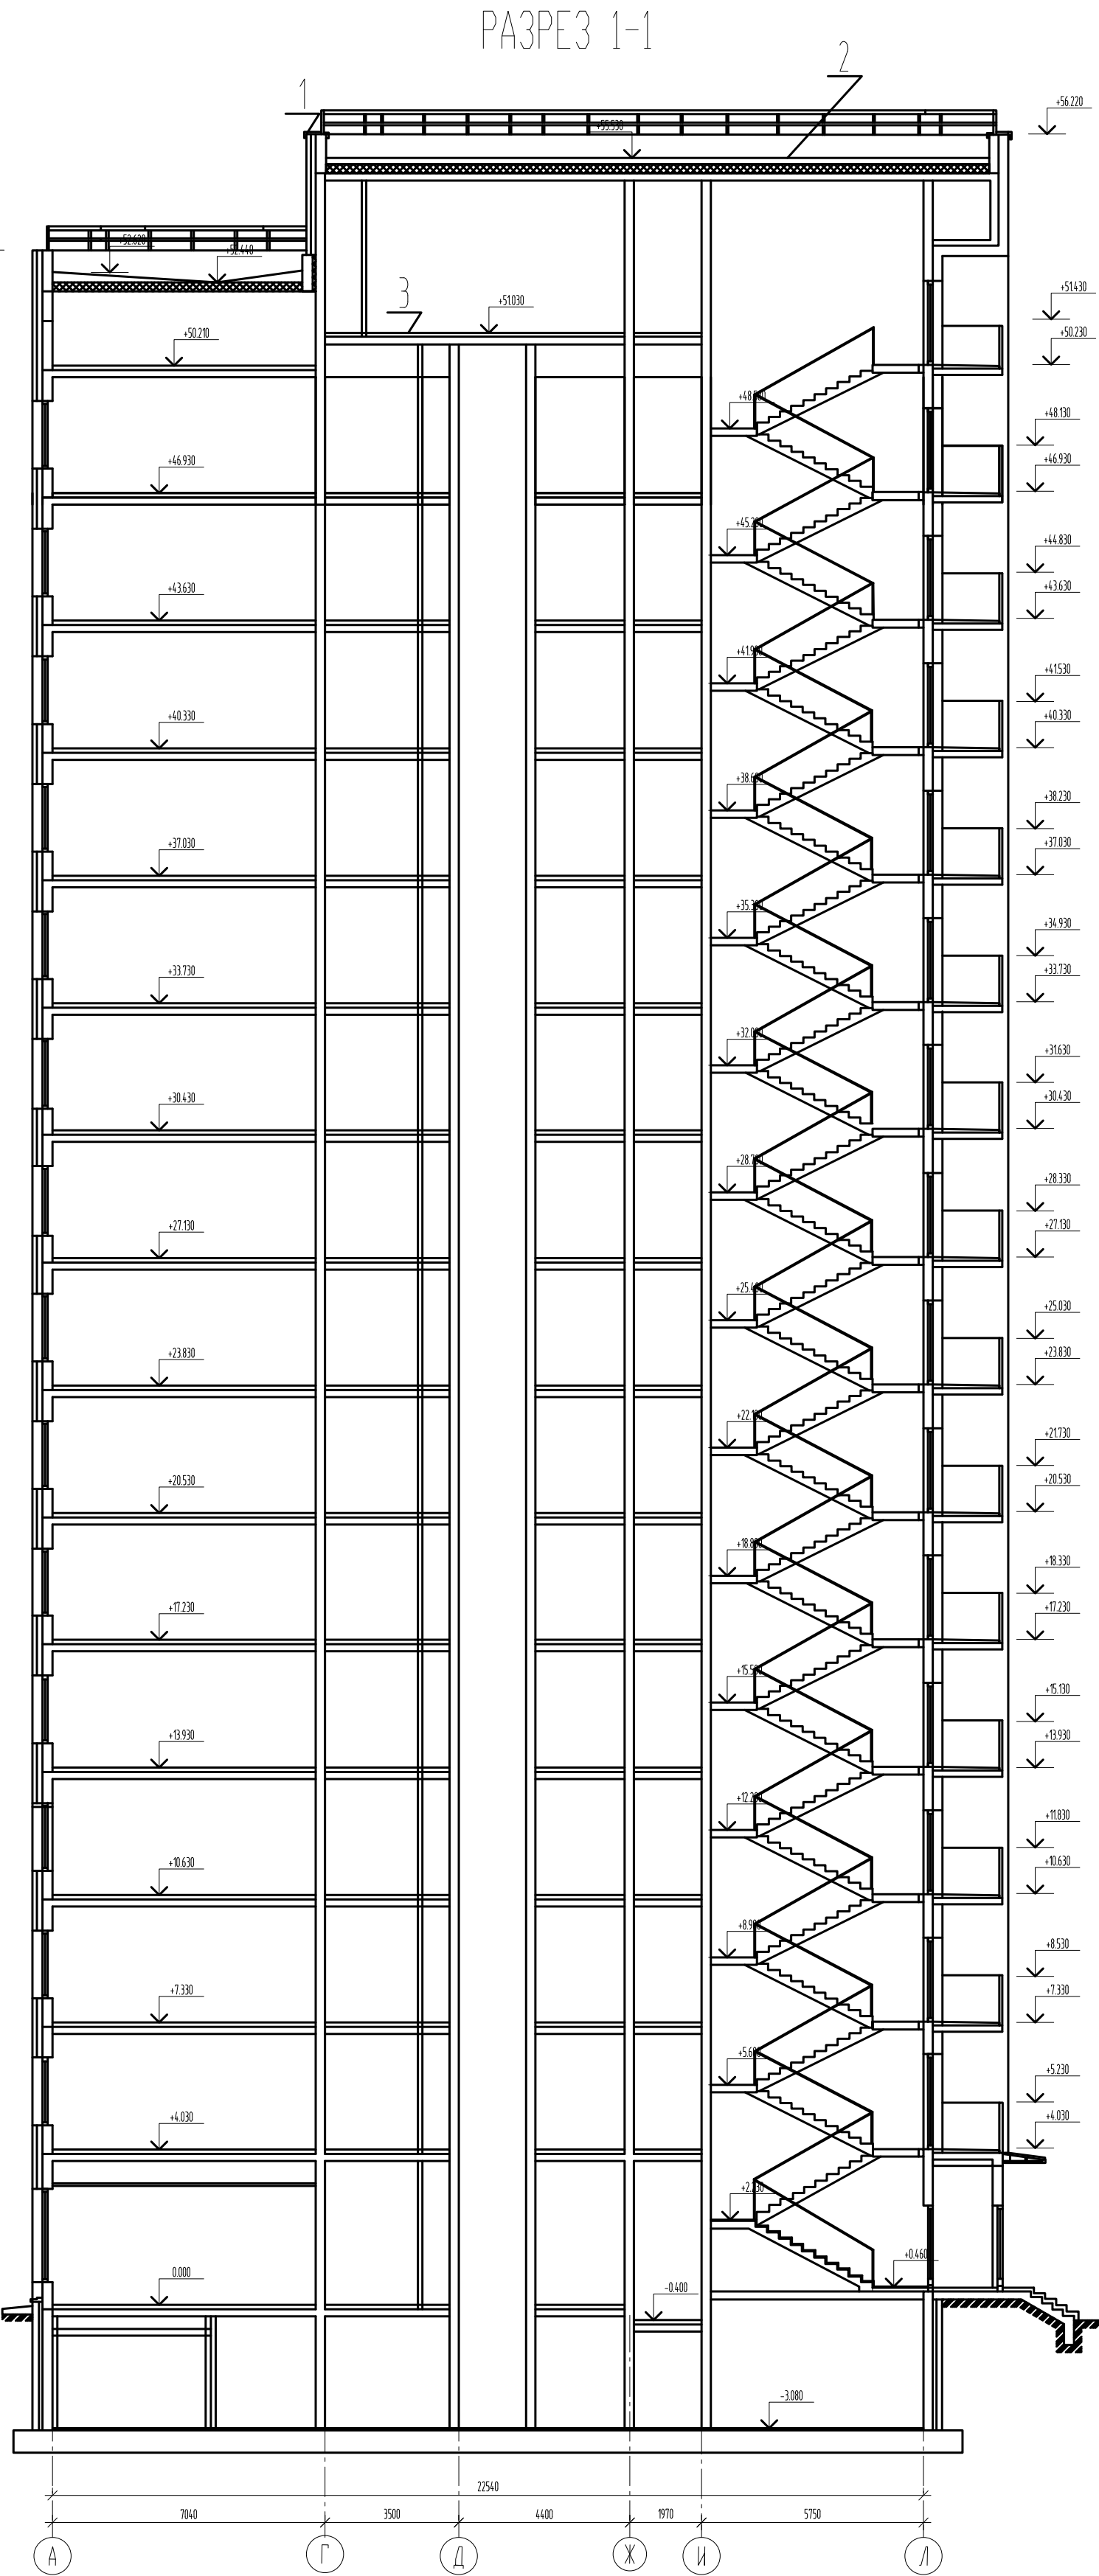

ЭКСПЛИКАЦИЯ ПОМЕЩЕНИЙ 1 ЭТАЖА		
п/п	НАИМЕНОВАНИЕ ПОМЕЩЕНИЯ	ПЛОЩАДЬ м²
1	Входная тамбур	5.14
2	Входная тамбур	11.96
3	Вестибюль	10.02
4	Помещение консьержа	10.37
5	Универсальный санузел	4.83
6	Помещение уборочного инвентаря	2.19
7	Литровой холл	12.12
8	Лестница	14.95
9	Тамбур	3.66
10	Мусоросборная камера	5.12
11	Коридор	11.69
НЕЖИЛЫЕ ПОМЕЩЕНИЯ		
14	Помещение общественного назначения	29.23
14.1	Санузел	4.92
14.2	Помещение уборочного инвентаря	1.72
15	Помещение общественного назначения	41.54
15.1	Санузел	4.97
15.2	Помещение уборочного инвентаря	2.79
16	Помещение общественного назначения	53.24
16.1	Санузел	5.06
16.2	Помещение уборочного инвентаря	3.62
17	Помещение общественного назначения	44.07
17.1	Санузел	4.97
17.2	Помещение уборочного инвентаря	2.31
18	Помещение общественного назначения	48.28
18.1	Санузел	5.9
18.2	Помещение уборочного инвентаря	2.79
19	Помещение общественного назначения	58.73
19.1	Санузел	5.79
19.2	Помещение уборочного инвентаря	2.68

ЭКСПЛИКАЦИЯ ПОМЕЩЕНИЙ ТИП. ЭТАЖА		
п/п	НАИМЕНОВАНИЕ ПОМЕЩЕНИЯ	ПЛОЩАДЬ м²
1	Литровой холл	14.19
2	Межквартирный коридор	64.3
3	Помещение мусоропровода	2.89
4	Тамбур	10.9
5	Лестница	15.01
6	ОДНОКОМНАТНАЯ КВАРТИРА	39.85
6.1	Прихожая	7.46
6.2	Комната	16.09
6.3	Кухня	8.31
6.4	Совмещенный санузел	4.22
7	ОДНОКОМНАТНАЯ КВАРТИРА	39.42
7.1	Прихожая	4.4
7.2	Комната	14.77
7.3	Кухня	11.73
7.4	Ванная комната	2.82
7.5	Санузел	1.44
8	ДВУХКОМНАТНАЯ КВАРТИРА	1
8.1	Прихожая	7.36
8.2	Комната	16.43
8.3	Комната	10.15
8.4	Кухня	11.66
8.5	Ванная комната	2.86
8.6	Санузел	1.41
9	ОДНОКОМНАТНАЯ КВАРТИРА	43.74
9.1	Прихожая	4.27
9.2	Комната	18.47
9.3	Кухня	12.08
9.4	Ванная комната	3.01
9.5	Санузел	1.48
10	ДВУХКОМНАТНАЯ КВАРТИРА	55.21
10.1	Прихожая	7.77
10.2	Комната	16.62
10.3	Комната	10.29
10.4	Кухня	11.53
10.5	Ванная комната	2.99
10.6	Санузел	1.49
11	ОДНОКОМНАТНАЯ КВАРТИРА	38.75
11.1	Прихожая	3.68
11.2	Комната	18.04
11.3	Кухня	12.4
11.4	Ванная комната	3.1
11.5	Санузел	1.43
12	ДВУХКОМНАТНЫЕ КВАРТИРЫ	62.46
12.1	Прихожая	6.08
12.2	Комната	18.77
12.3	Комната	15
12.4	Кухня	11.66
12.5	Ванная комната	2.95
12.6	Санузел	1.39
12.7	Кладовая	2.36
13	ОТКРЫТАЯ ЛОДЖИЯ	5.96

КП 08.02.01 ПД-31			
АРХИТЕКТУРНО-СТРОИТЕЛЬНАЯ ЧАСТЬ			
МНОГОЭТАЖНЫЙ ДОМ			
ДОЛЖНОСТЬ	ФАМИЛИЯ	ПОДПИСЬ	ДАТА
ВЫПОЛНИЛ	ГЛАЖКОВА И.А.		
РАСЧЕТОМ	ЖИГАЛЕНКО И.В.		
ПРОЕКТ	САМОУХОВА О.И.		
ТРЕБОВАЛ	ЖИГАЛЕНКО И.В.		
План 1-го и типового этажей; Фасад 14-1; Разрез 1-1; Генплан и 1:500; Экспликация помещений/генплана; Спецификация окон и дверей			
КАС №7			