


СТРОИТЕЛЬНЫЙ ГЕНЕРАЛЬНЫЙ ПЛАН

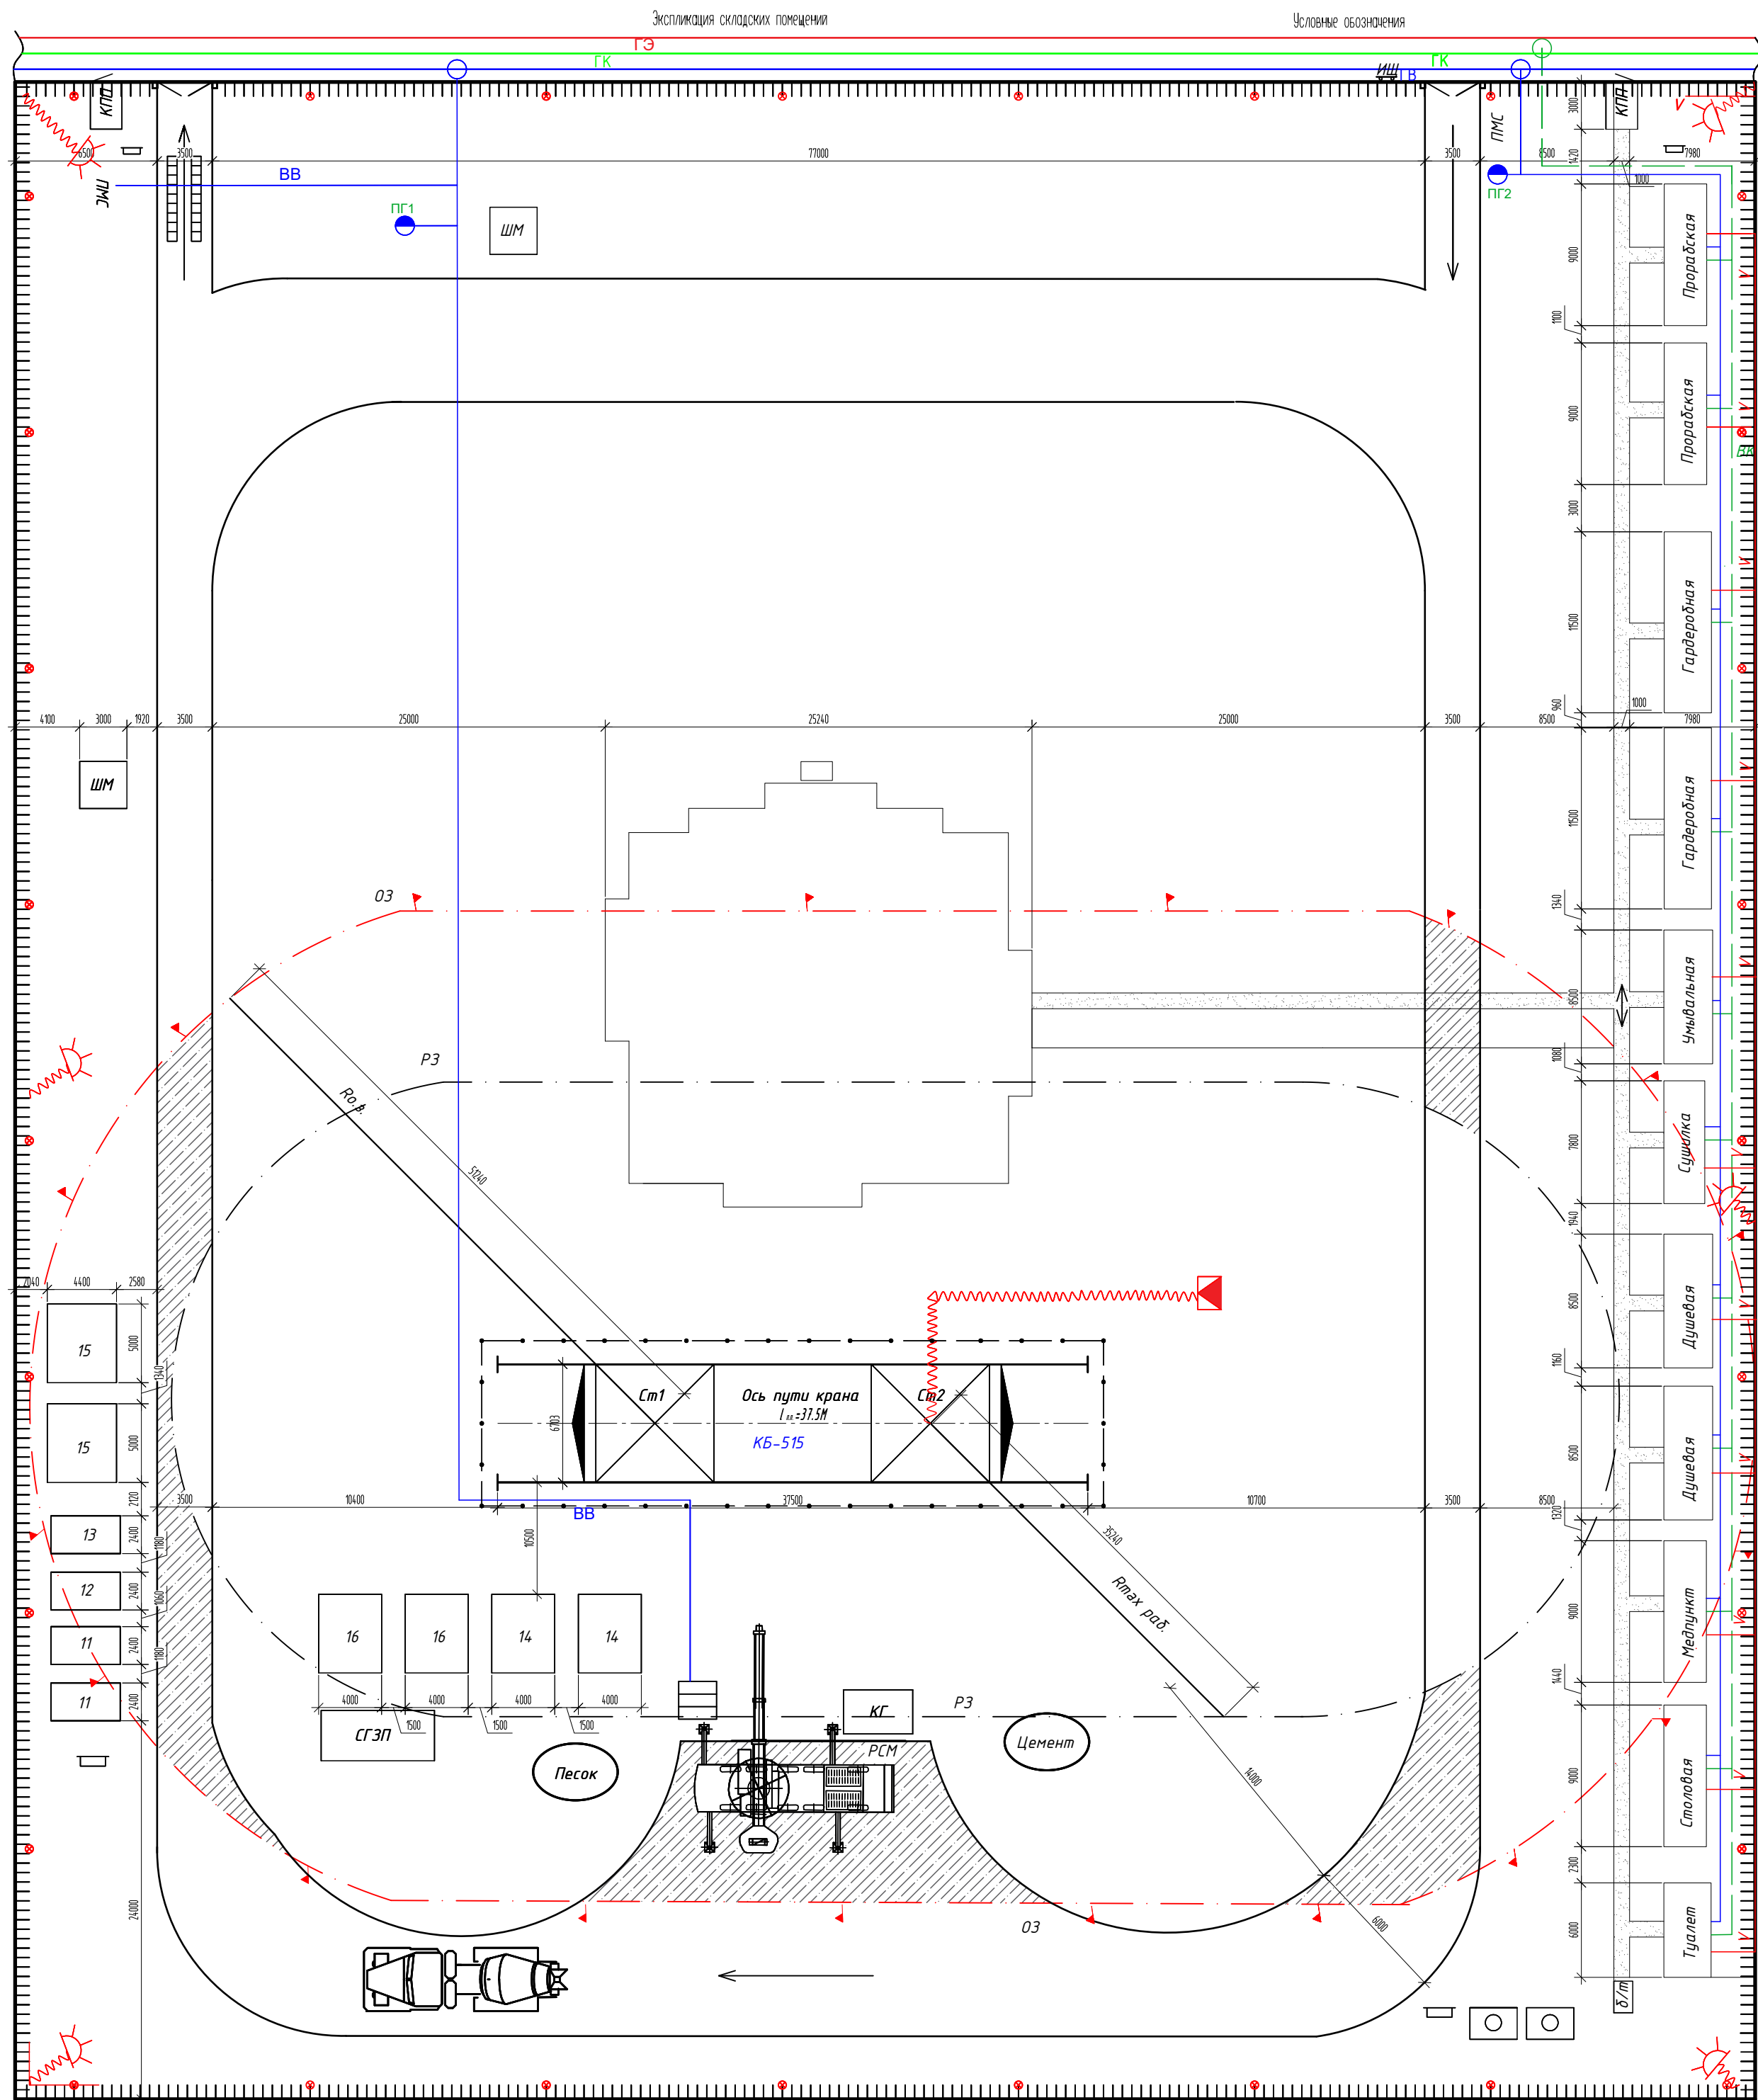

УСЛОВНЫЕ ОБОЗНАЧЕНИЯ

ЭКСПЛИКАЦИЯ СКЛАДСКИХ ПОМЕЩЕНИЙ

ГЗ	Городская энергосеть	ГВ	Городской водопровод	ШМ	Штепсельный кабель	●	Фокус
W	Синхронная энергосеть	ВВ	Временный водопровод	□	Место для крана	—○—	Гидрот
V	Общественная энергосеть	ВБ	Проектируемый водопровод	□	Проектируемый ствол со средними параметрами	—○—	Ворота
Т	Трансформатор ТМ-100/10	В	Канализационный водопровод		Ограждение	□	Назначение воды
ГК	Городская канализация	РЗ	Рабочая зона крана	—	Информационный щит	—	Ограждение крана
ВК	Временная канализация	ОЗ	Опасная зона	—	Посыпание дорожки	—	Ограждение здания
ЛК	Проектируемая канализация	ОЗП	Опасная зона подготовки части	—	Временная дорожка	КГ	Контрольный ступ
К	Канализационный колодец	ПМС	Площадка для мойки колес	—	Проектор	СГЗП	Средств защиты окружающей среды

№	Назначение	Тип привода
10	Кран	Открытый ствол
11	Временная вода	Навес
12	Окрасочная камера	Навес
13	Коррозия	Навес
14	Амортизатор	Закрытый ствол
15	Минеральная вода	Закрытый ствол
16	Очистка	Открытый ствол

ТЕХНИКО-ЭКОНОМИЧЕСКИЕ ПОКАЗАТЕЛИ

№	Назначение	Ед. изм.	Показатель
1	Площадь строительной площадки	м²	356,18
2	Площадь застройки проектируемого здания	м²	547,72
3	Площадь застройки временных зданий	м²	484,54
4	Протяженность временных дорог	м	138,2
5	Протяженность электросетевой линии	м	239,8
6	Протяженность временного водопровода	м	117,4
7	Протяженность временной канализации	м	117,4
8	Протяженность временной осветительной линии	м	239,34
9	Протяженность временного ограждения	м	350,61
10	Коэффициент Кв.б.	%	88
11	Кв.б.	%	88


ТЕХ. ХАРАКТЕРИСТИКИ КРАНА КБ-515

ГРУЗОВАЯ ПОДЪЕМНОСТЬ	10Т
ВЫСОТА ПОДЪЕМА	90М
ВЫСЕТ СТРЕЛЫ	72М
ЗАДВИЖКА	50М

ТЕХ. ХАРАКТЕРИСТИКИ ПОДЪЕМНИКА ПР-1772А

ГРУЗОВАЯ ПОДЪЕМНОСТЬ	580 кг
ВЫСОТА ПОДЪЕМА	70 М
ГАБАРИТ КАБИНЫ	2/1,2/2,4 М
СКОРОСТЬ ОБЪЕМА	0,5 М/СЕК

ПРИМЕЧАНИЕ
Строительный план разработан на основании части здания, монтаж фундамента КБ-515
Q = 40 т
L = 40 м
H = 70 м

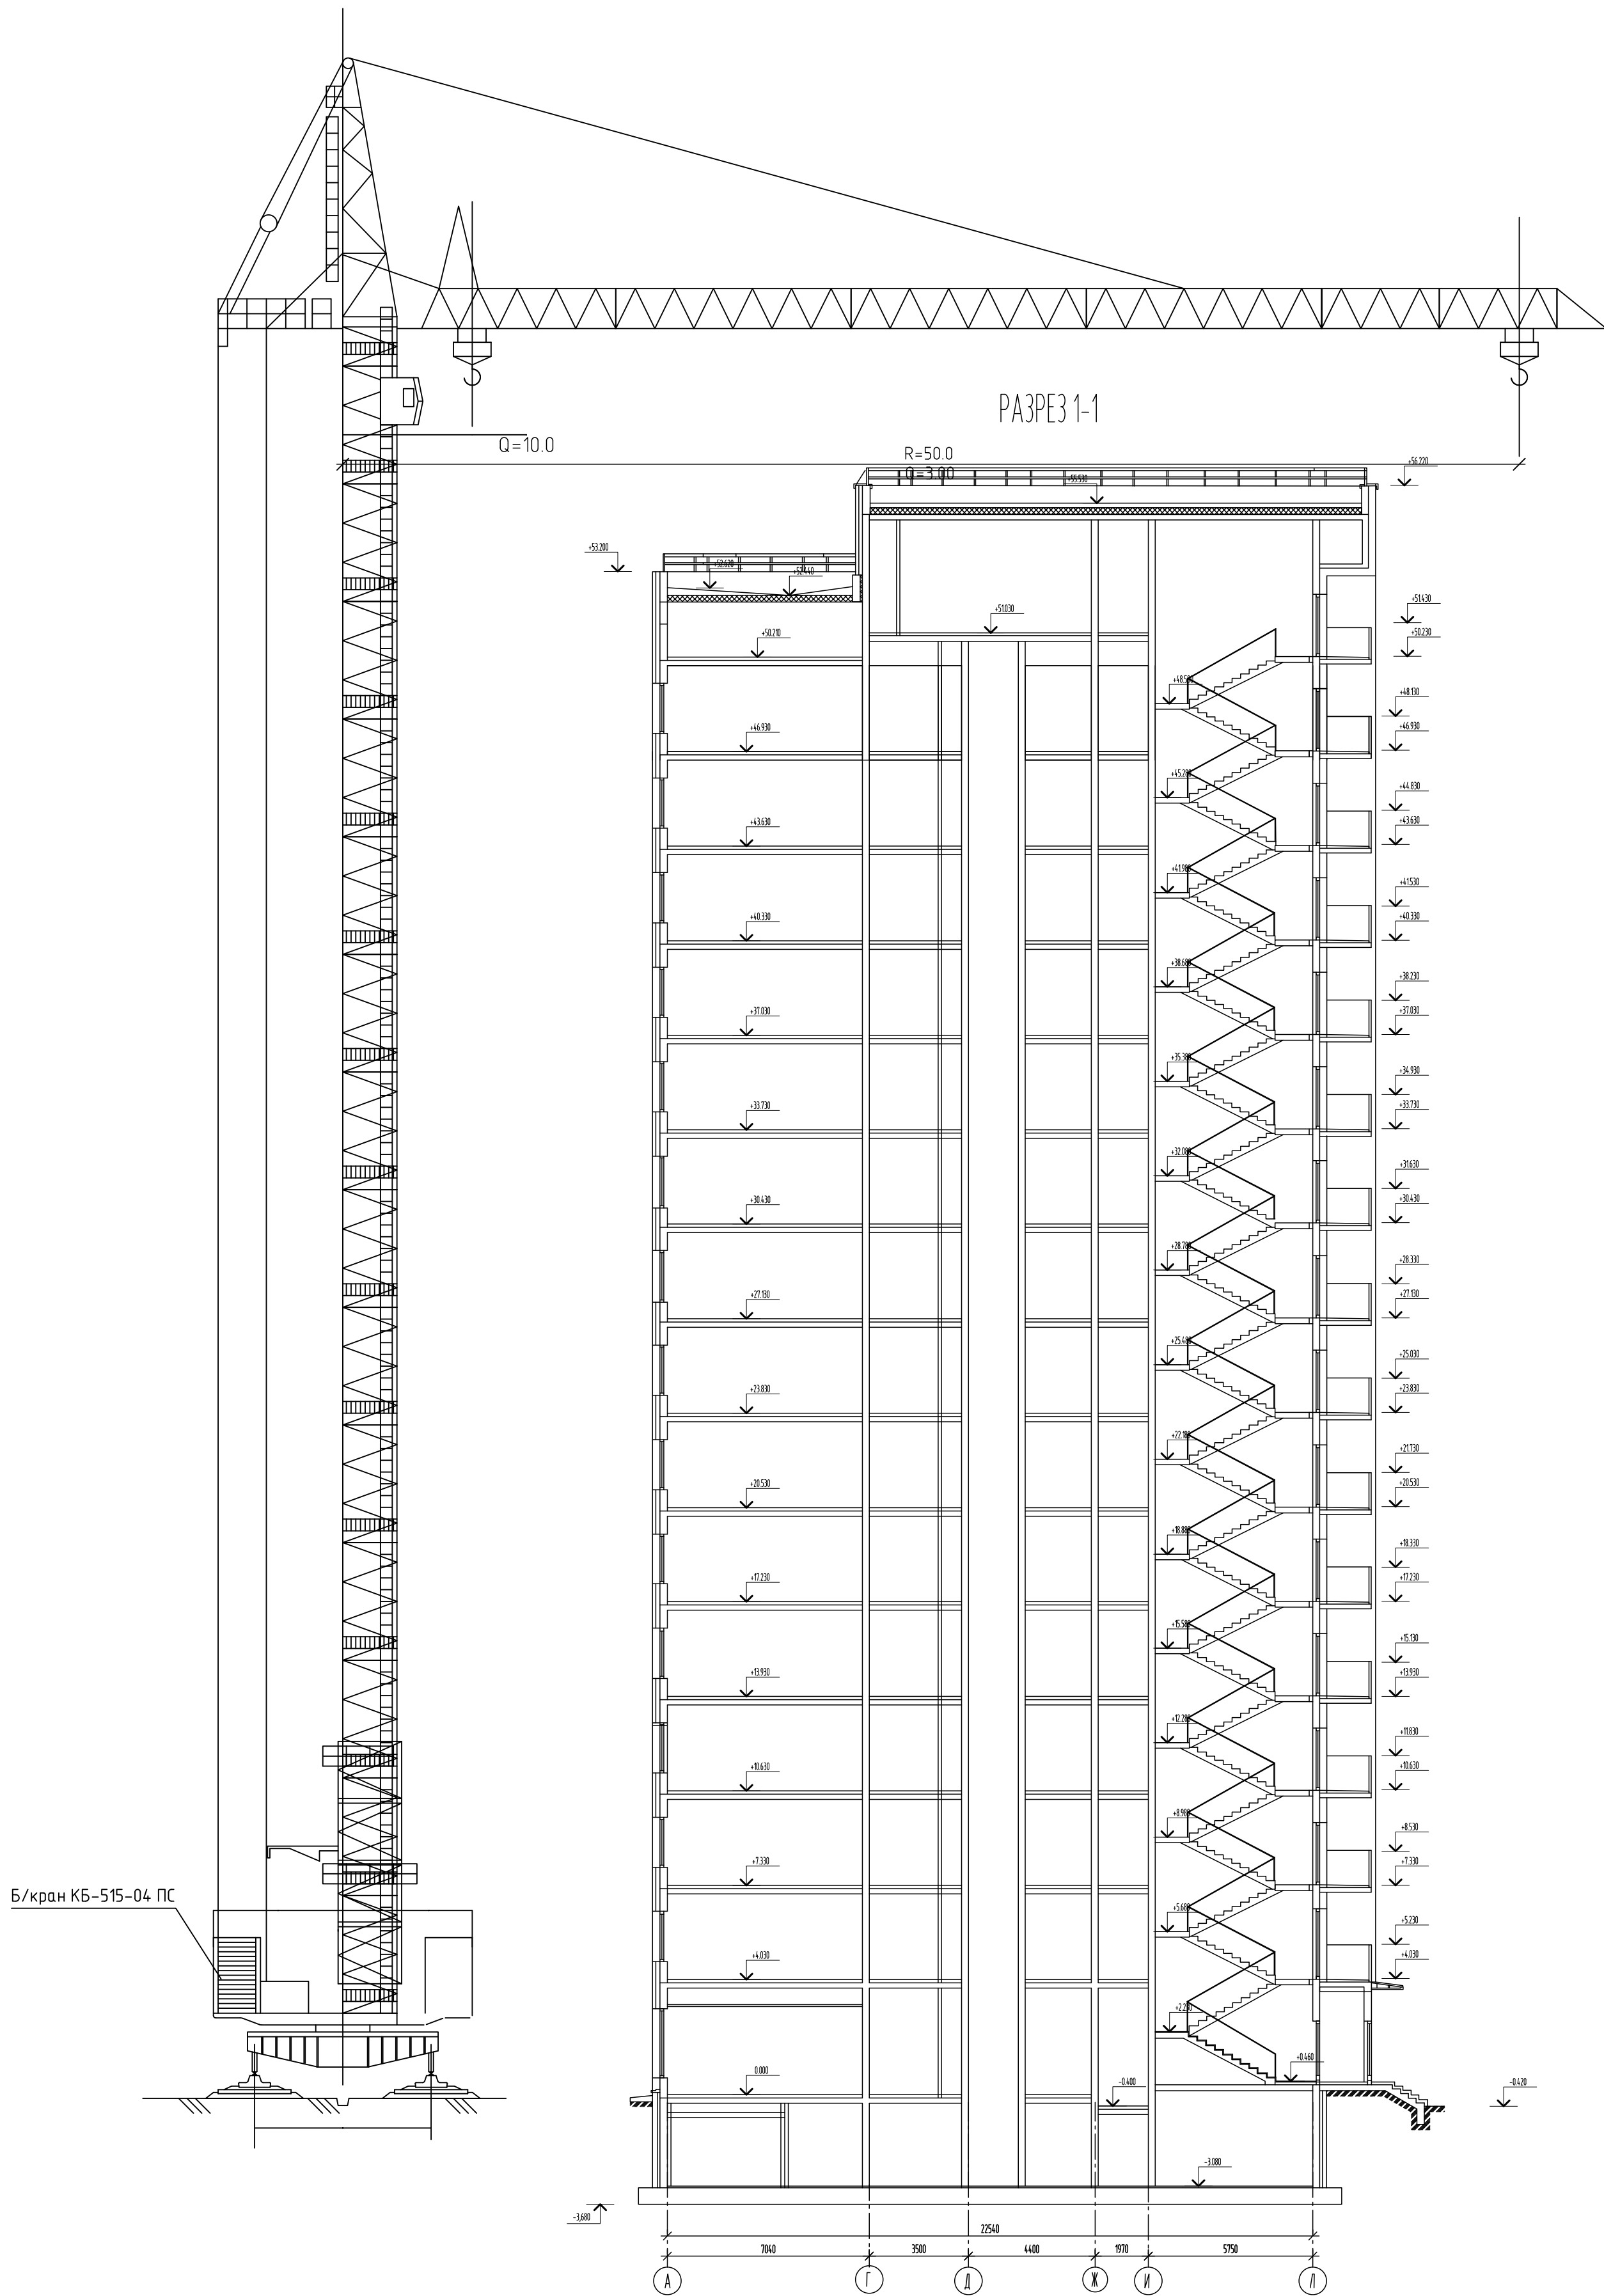

КП 08.02.01 ПД-31			
ОРГАНИЗАЦИОННО-ТЕХНОЛОГИЧЕСКАЯ ЧАСТЬ			
ДОЛЖНОСТЬ	ФАМИЛИЯ	ПОДПИСЬ	ДАТА
ВЫПОЛНИЛ	ГЛАВНОУЧАЩИЙСЯ	1	5