
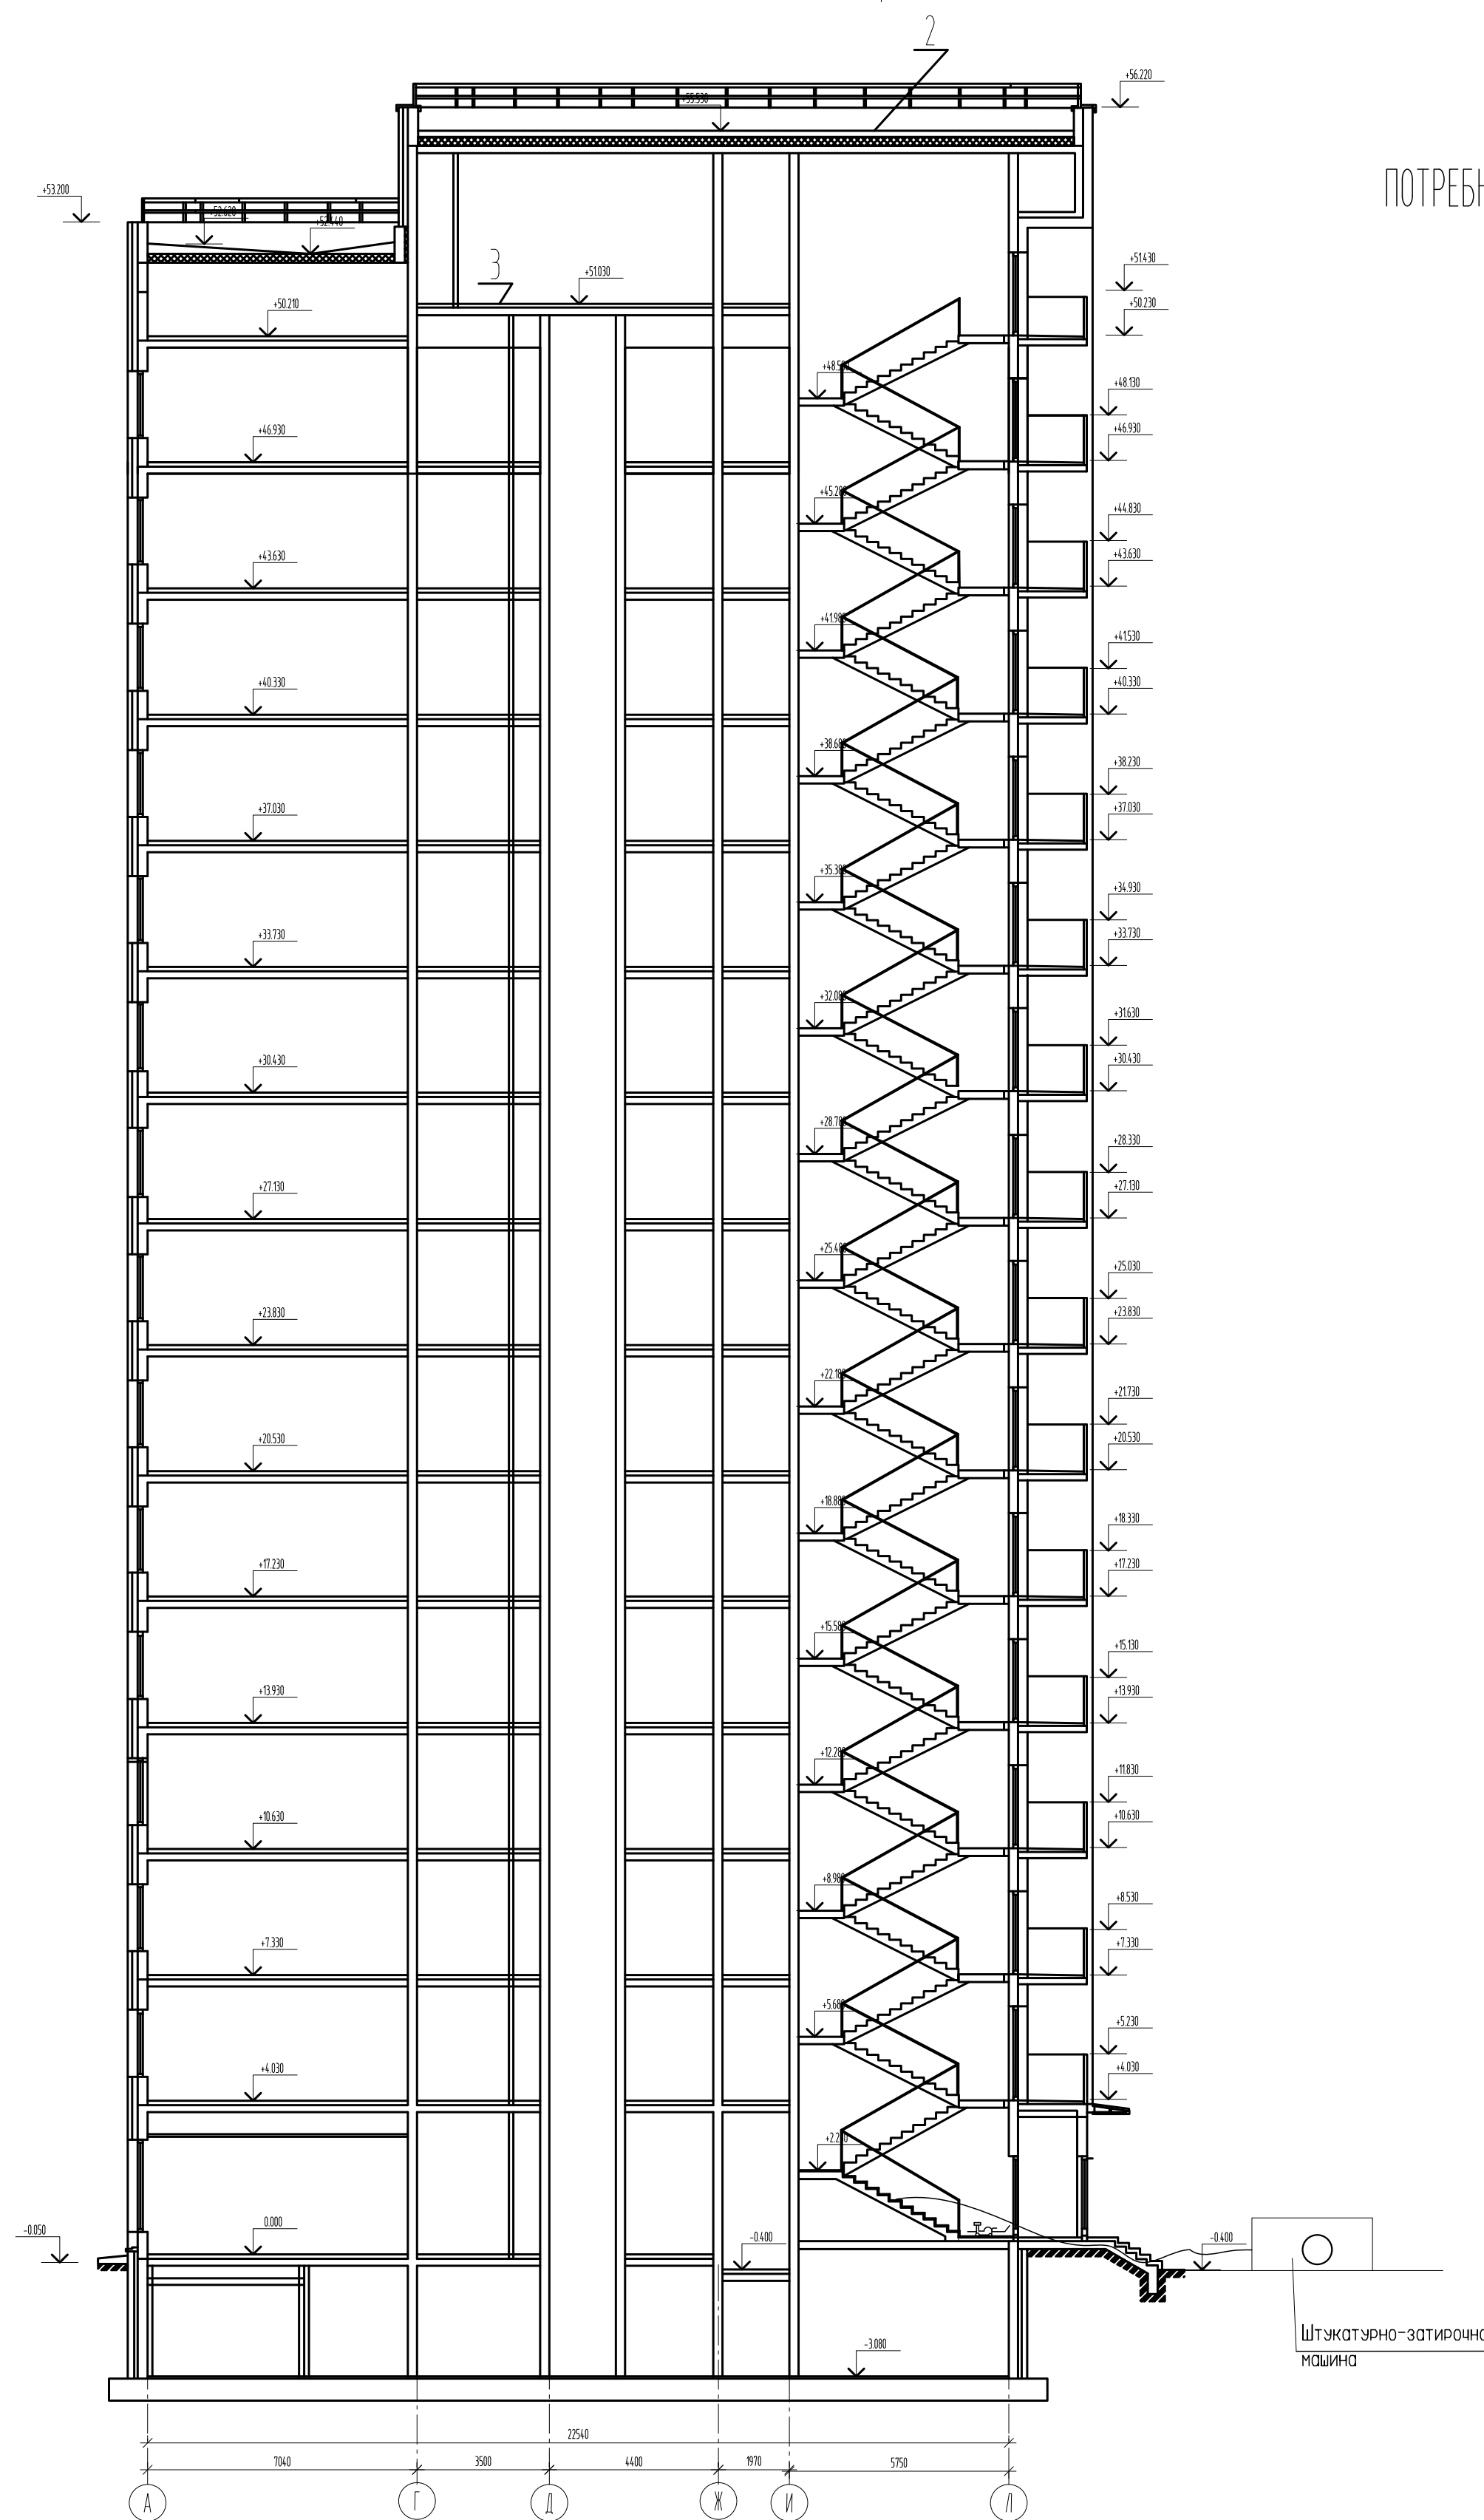


ПОСЛЕДОВАТЕЛЬНОСТЬ ПРОИЗВОДСТВА ШТУКАТУРНЫХ РАБОТ. СХЕМА МЕХАНИЗИРОВАННОЙ ПОДАЧИ РАСТВОРА И РАЗМЕЩЕНИЯ МЕХАНИЗМОВ НА ЭТАЖАХ

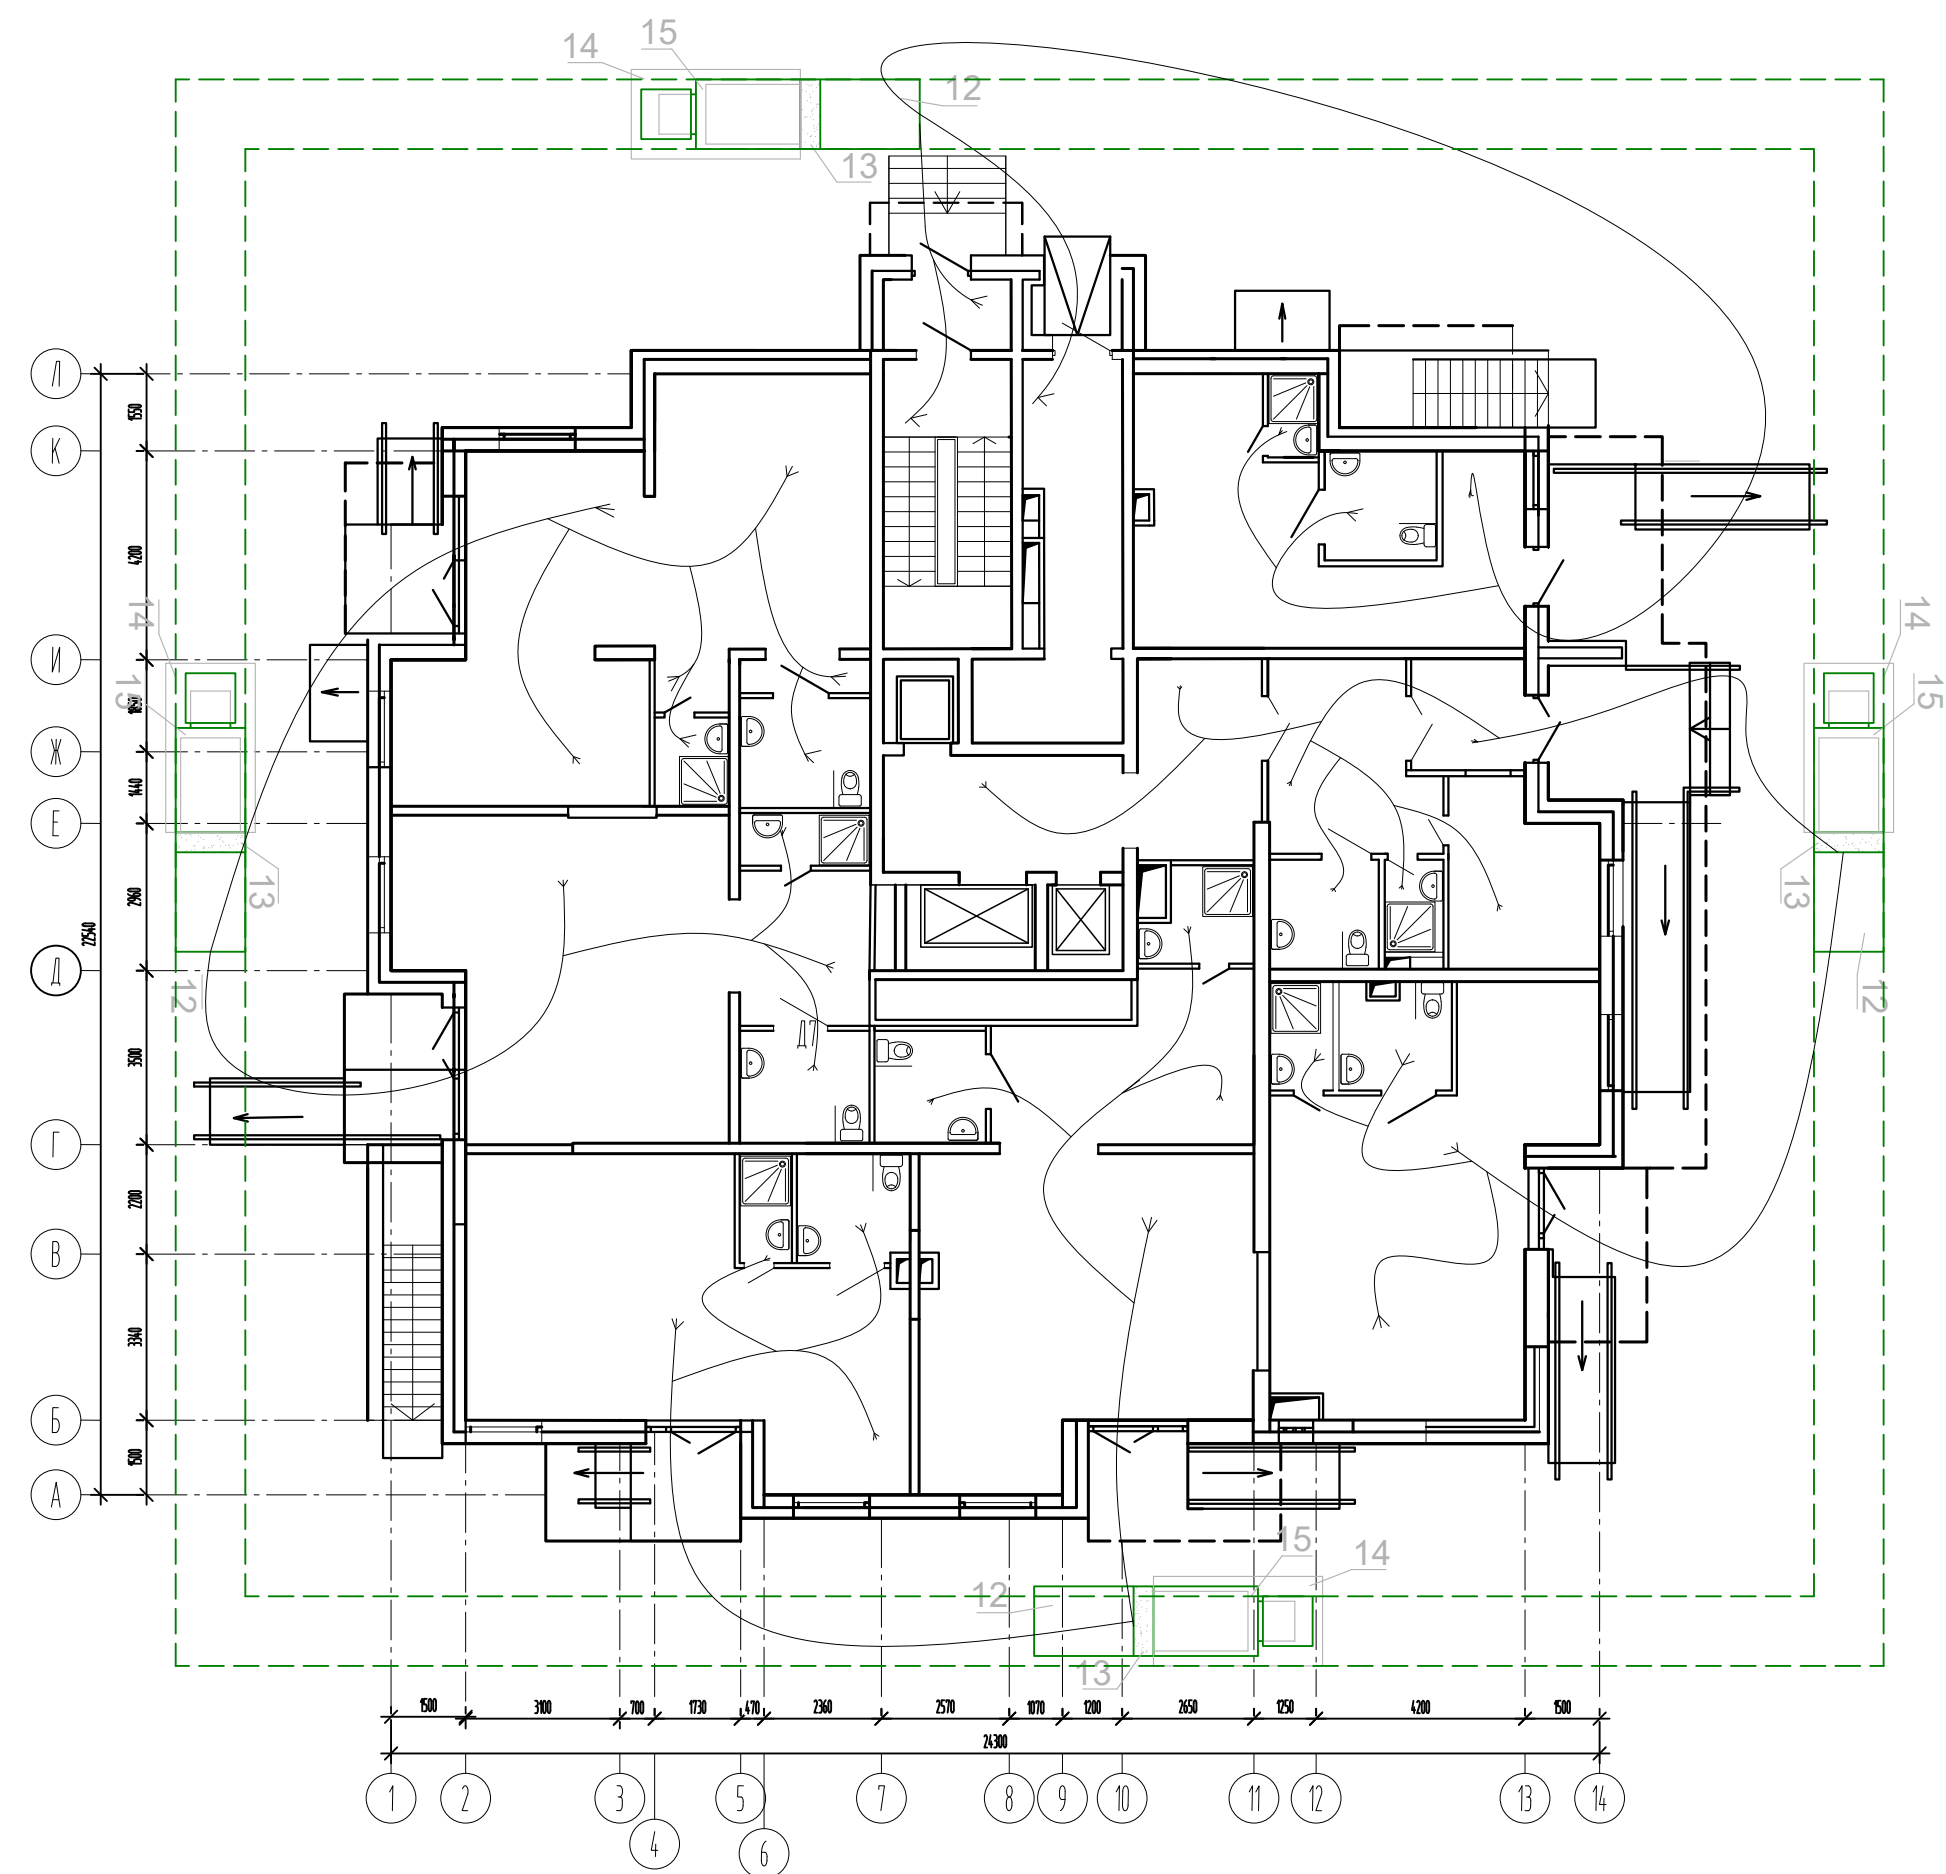

ПОТРЕБНОСТЬ В МАШИНАХ, ОБОРУДОВАНИИ, ИНСТРУМЕНТАХ И ПРИСПОСОБЛЕНИЯХ

Наименование	Обозначение стандарта, номер чертежа, тип	Количество
Шпунтовая свинция	ПШ-2М, 4М/4	1
Трансформатор	ИВ-4	1
Преобразователь частоты тока	ИВ-3401	1
Машина шпунтовая-защитная	О-86	6
Устройство для подачи воды к запыленным машинам		6
Удочка для нанесения лакокрасочного слоя		3
Бескомпрессорная форсунка	ГОСТ 10466-95	
Калька шпунтурная	ГОСТ 9533-91	10
Кобы шпунтурный	ГОСТ 7945-93	5
Отрезная ОИ-1	ГОСТ 9533-91	5
Скоба дилематическая	ОТУ 12-497-87	35
Молоток шпунтурный	ГОСТ 10642-93	10
Острогины	ГОСТ 7282-95	2
Нок для шпунтурных работ	ГОСТ 18975-93	2
Терка деревянная		35
Терка бочажная		35
Пробило диаметр 2 м	ГОСТ 25482-93	6
Пробило увеличение	ГОСТ 25482-93	6
Пробило пазовое	ГОСТ 25482-93	6
Полукругок деревянный 350 и 500 мм		10
Лопата разборная	ГОСТ 3620-96	6
Рукоятка потолочная одностронняя	ГОСТ 15995-88	6
Рукоятка потолочная двухсторонняя	ГОСТ 15995-88	6
Лопок для сбора отработанного раствора		10
Резка с откосом	ГОСТ 9416-93	6
Уровень строительный	ГОСТ 9416-93	6
Откос (0-400)	ГОСТ 7948-90	6
Метр складной	ГОСТ 7948-90	6
Ящик металлический на колесах емкость 0,35м³	Сейфст. изометалл	
Ведро	ГОСТ 20558-92	13
Поручки резные, пар	ГОСТ 20009-94	22
Очки защитные	ГОСТ 12.4.013-95	12
Работа резные: ширина: - Ø 51 мм	ГОСТ 86691-89	40
	Ø 30 мм	40
	Ø 15 мм	40
	Ø 10 мм	20
	Ø 12 мм	20
Подмости универсальные сборно-разборные		6
Столбы универсальные		12
Столбы 2-х-х. Высотами 3м/4м		12

ТЕХНИЧЕСКИЕ ХАРАКТЕРИСТИКИ ШТУКАТУРНОЙ СТАНЦИИ



	Параметры	Значение
1	Производительность м/ч	4
2	Вместимость думпекр м	2500
3	Длина секции подачи растора по вертикали	30
4	Напряжение кВт	5-30
5	Габаритные размеры мм	4/25
6	Масса кг	3800

ТЕХНИКО-ЭКОНОМИЧЕСКИЕ ПОКАЗАТЕЛИ

№п/п	Показатели	Единица измерения	Колич.	Примечания
1	Зарплата поощр.	чел.-день	5436,79	
2	Продолжительность	дня	103	
3	Выработка на одного рабочего в смену	чел.-дней/м ²	0,61	
4	Полученная выработка	г	171	

УСЛОВНЫЕ ОБОЗНАЧЕНИЯ

3-рубли для подачи расстора, 4-соло, 5-лоток для сбора опавшего рас- тора, 6-ящик для расстора, 7-кадель к запрячным машинам, 8-запрячные машины, 9-стопик-подмости, 10-позатыки электропиз, 11-правило длины 2м, 12-универсальная станица, 13-приемный бункер, 14-идентифицирующая подмус, 15-самосвал, 16-хл-очередность отгрузки помещенци, ш-рабочее место шпикатора.

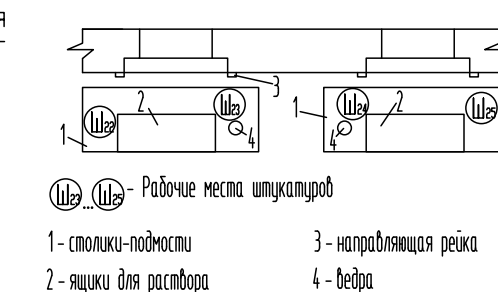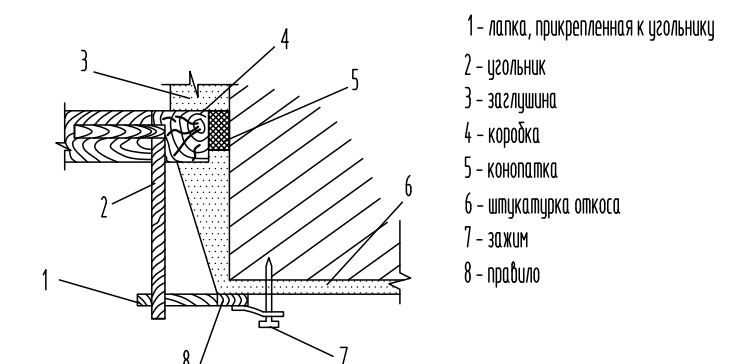ОРГАНИЗАЦИЯ РАБОЧЕГО МЕСТА
ДЛЯ ОШТУКАТУРИВАНИЯ ОТКОСОВУГОЛЬНИК ДЛЯ ОПРЕДЕЛЕНИЯ
УГЛА РАССВЕТА НА ОТКОСАХ

КАЛЬКУЛЯЦИЯ ЗАТРАТ ТРУДА, ГРАФИК ПРОИЗВОДСТВ РАБОТ

[illegible]

					КП 08.02.01 ПД-31		
					КОНСТРУКТИВНАЯ ЧАСТЬ		
ДОЛЖНОСТЬ	ФАМИЛИЯ	ПОДПИСЬ	ДАТА		МНОГОЭТАЖНЫЙ ДОМ		
					СТАДИЯ	ЛИСТ	ЛИСТОВ
					У	2	5
ВЫПОЛНИЛ	ГЛАЗКОВА М.А.				ПЛАН ПЕРЕКРЫТИЙ И ПОКРЫТИЙ, ПЛАН ПОДВАЛА, ПЛАН ФУНДАМЕНТА, ПЛАН КРОВЛИ, ЭЛЕ 1, 2, 3, ЭКСПЛИКАЦИЯ ПОМЕЩЕНИЙ ПОДАВА		
РАСЧИСЛЯЕТ	ЖИЧЕНКОВА И.В.						
КОНЧИТ	САДОРНОВА О.М.						
ПРОВЕРЯЕТ	ЖИЧЕНКОВА И.						
					КАС №7		