


СТРОИТЕЛЬНЫЙ ГЕНЕРАЛЬНЫЙ ПЛАН

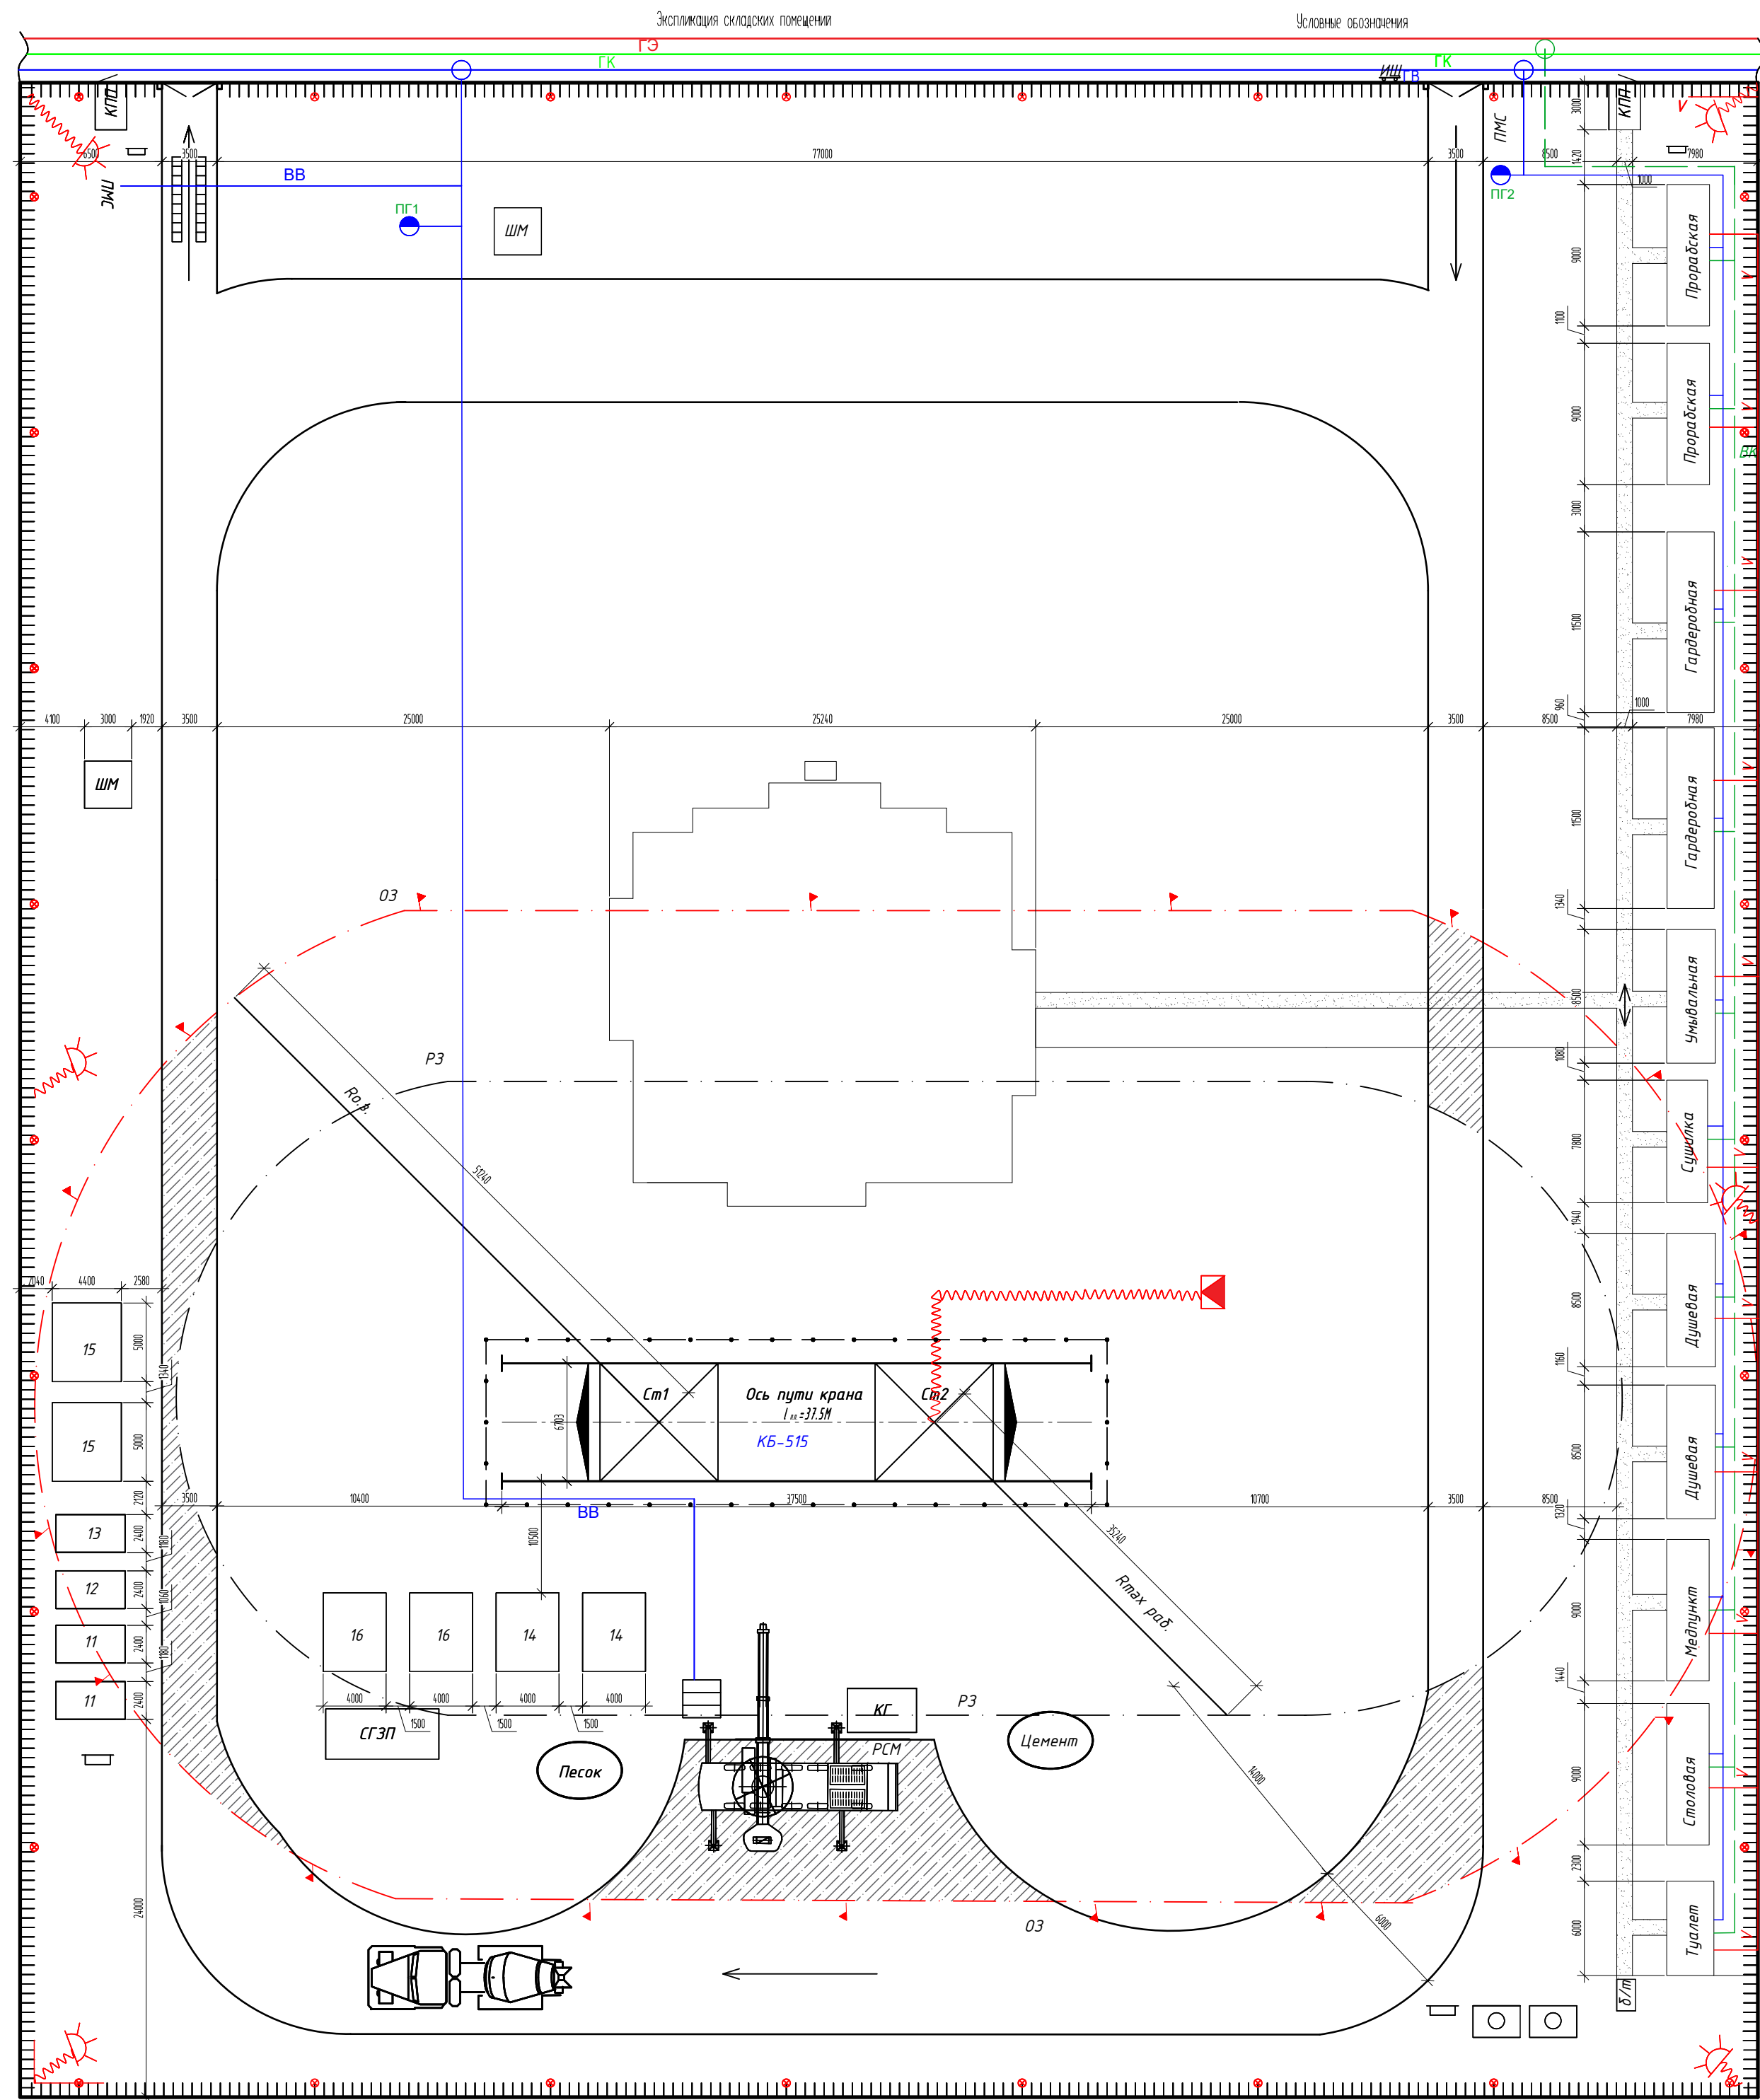

УСЛОВНЫЕ ОБОЗНАЧЕНИЯ				ЭКСПЛИКАЦИЯ СКЛАДСКИХ ПОМЕЩЕНИЙ			
ГЗ —	Городская электросеть	ГВ —	Городские водопровод	ШМ	Штепсельный кабель		Фонарь
ИММ	Сельская электросеть	ВВ —	Внутренние водопровод		Место для скрутки		Габарит
— —	Внутренняя электросеть	ВВ —	Прокладываемый водопровод		Прокладываемый канал со скрутками поперечником		Ворота
	Трансформатор ТН-100/10		Осушение		Осушение		Наполнение воды
ГК —	Городская канализация	РЗ	Разделенные зоны		Информационный кабель		Осушение крыши
ВК —	Внутренняя канализация	ОЗ	Отделенная зона		Полосовый кабель		Осушение здания
ВК —	Прокладываемая канализация	ОЗПВ	Отделенная зона поперечником		Внутренний кабель	КГ	Кабельный путь
	Канализация канализации	ПМК	Полосовый кабель канализации		Примечание	СЗП	Специальные служебные дорожные знаки

№	Наименование	Тип хранения
10	Карточка	Открытый склад
11	Деревянные бревна	Настил
12	Осыпные бревна	Настил
13	Кедровые бревна	Настил
14	Лесоматериал	Закрытый склад
15	Минеральные ваты	Закрытый склад
16	Пиломатериал	Открытый склад

ТЕХ. ХАРАКТЕРИСТИКИ КРАНА КБ-515

ГРУЗОПОДЪЕМНОСТЬ	10Т
ВЫСОТА ПОДЪЕМА	90.2М
ВЫУЕТ СТРЕЛЫ	72.4М
ЗАДНИЙ ГАБАРИТ	5.5М
КОЛЕЯ И БАЗА	7,5x7,5М


ТЕХ. ХАРАКТЕРИСТИКА ПОДЪЕМНИКА
ПР1-172А

ГРУЗОПОДЪЕМНОСТЬ	580 кг
ВЫСОТА ПОДЪЕМА	70 м
ГАБАРИТ КАБИНЫ	2/1,2/2,4м
СКОРОСТЬ ОБЪЕМА	0,5м/сек
МОЩНОСТЬ	12кВт

ПРИМЕЧАНИЕ
 План разработан на
 часть здания, монтаж
 кран КБ-515
 $Q = 10 \text{ т.}$
 $L = 40 \text{ м}$
 $H = 72,1 \text{ м}$

ТЕХНИКО-ЭКОНОМИЧЕСКИЕ ПОКАЗАТЕЛИ

№	Наименование	Ед. изм.	Показатель
1	Площадь строительных площадок	м ²	356218
2	Площадь застройки проектируемого здания	м ²	547,72
3	Площадь застройки временных зданий	м ²	484,54
4	Протяженность временных дорог	м	138,2
5	Протяженность электрических линий	м	239,8
6	Протяженность временного водопровода	м	177,4
7	Протяженность временной канализации	м	177,4
8	Протяженность временной осветительной линии	м	239,34
9	Протяженность временного ограждения	м	350,61
10	Коэффициент Кп.б.	%	88
11	K1	%	15
12	K2	%	1,36

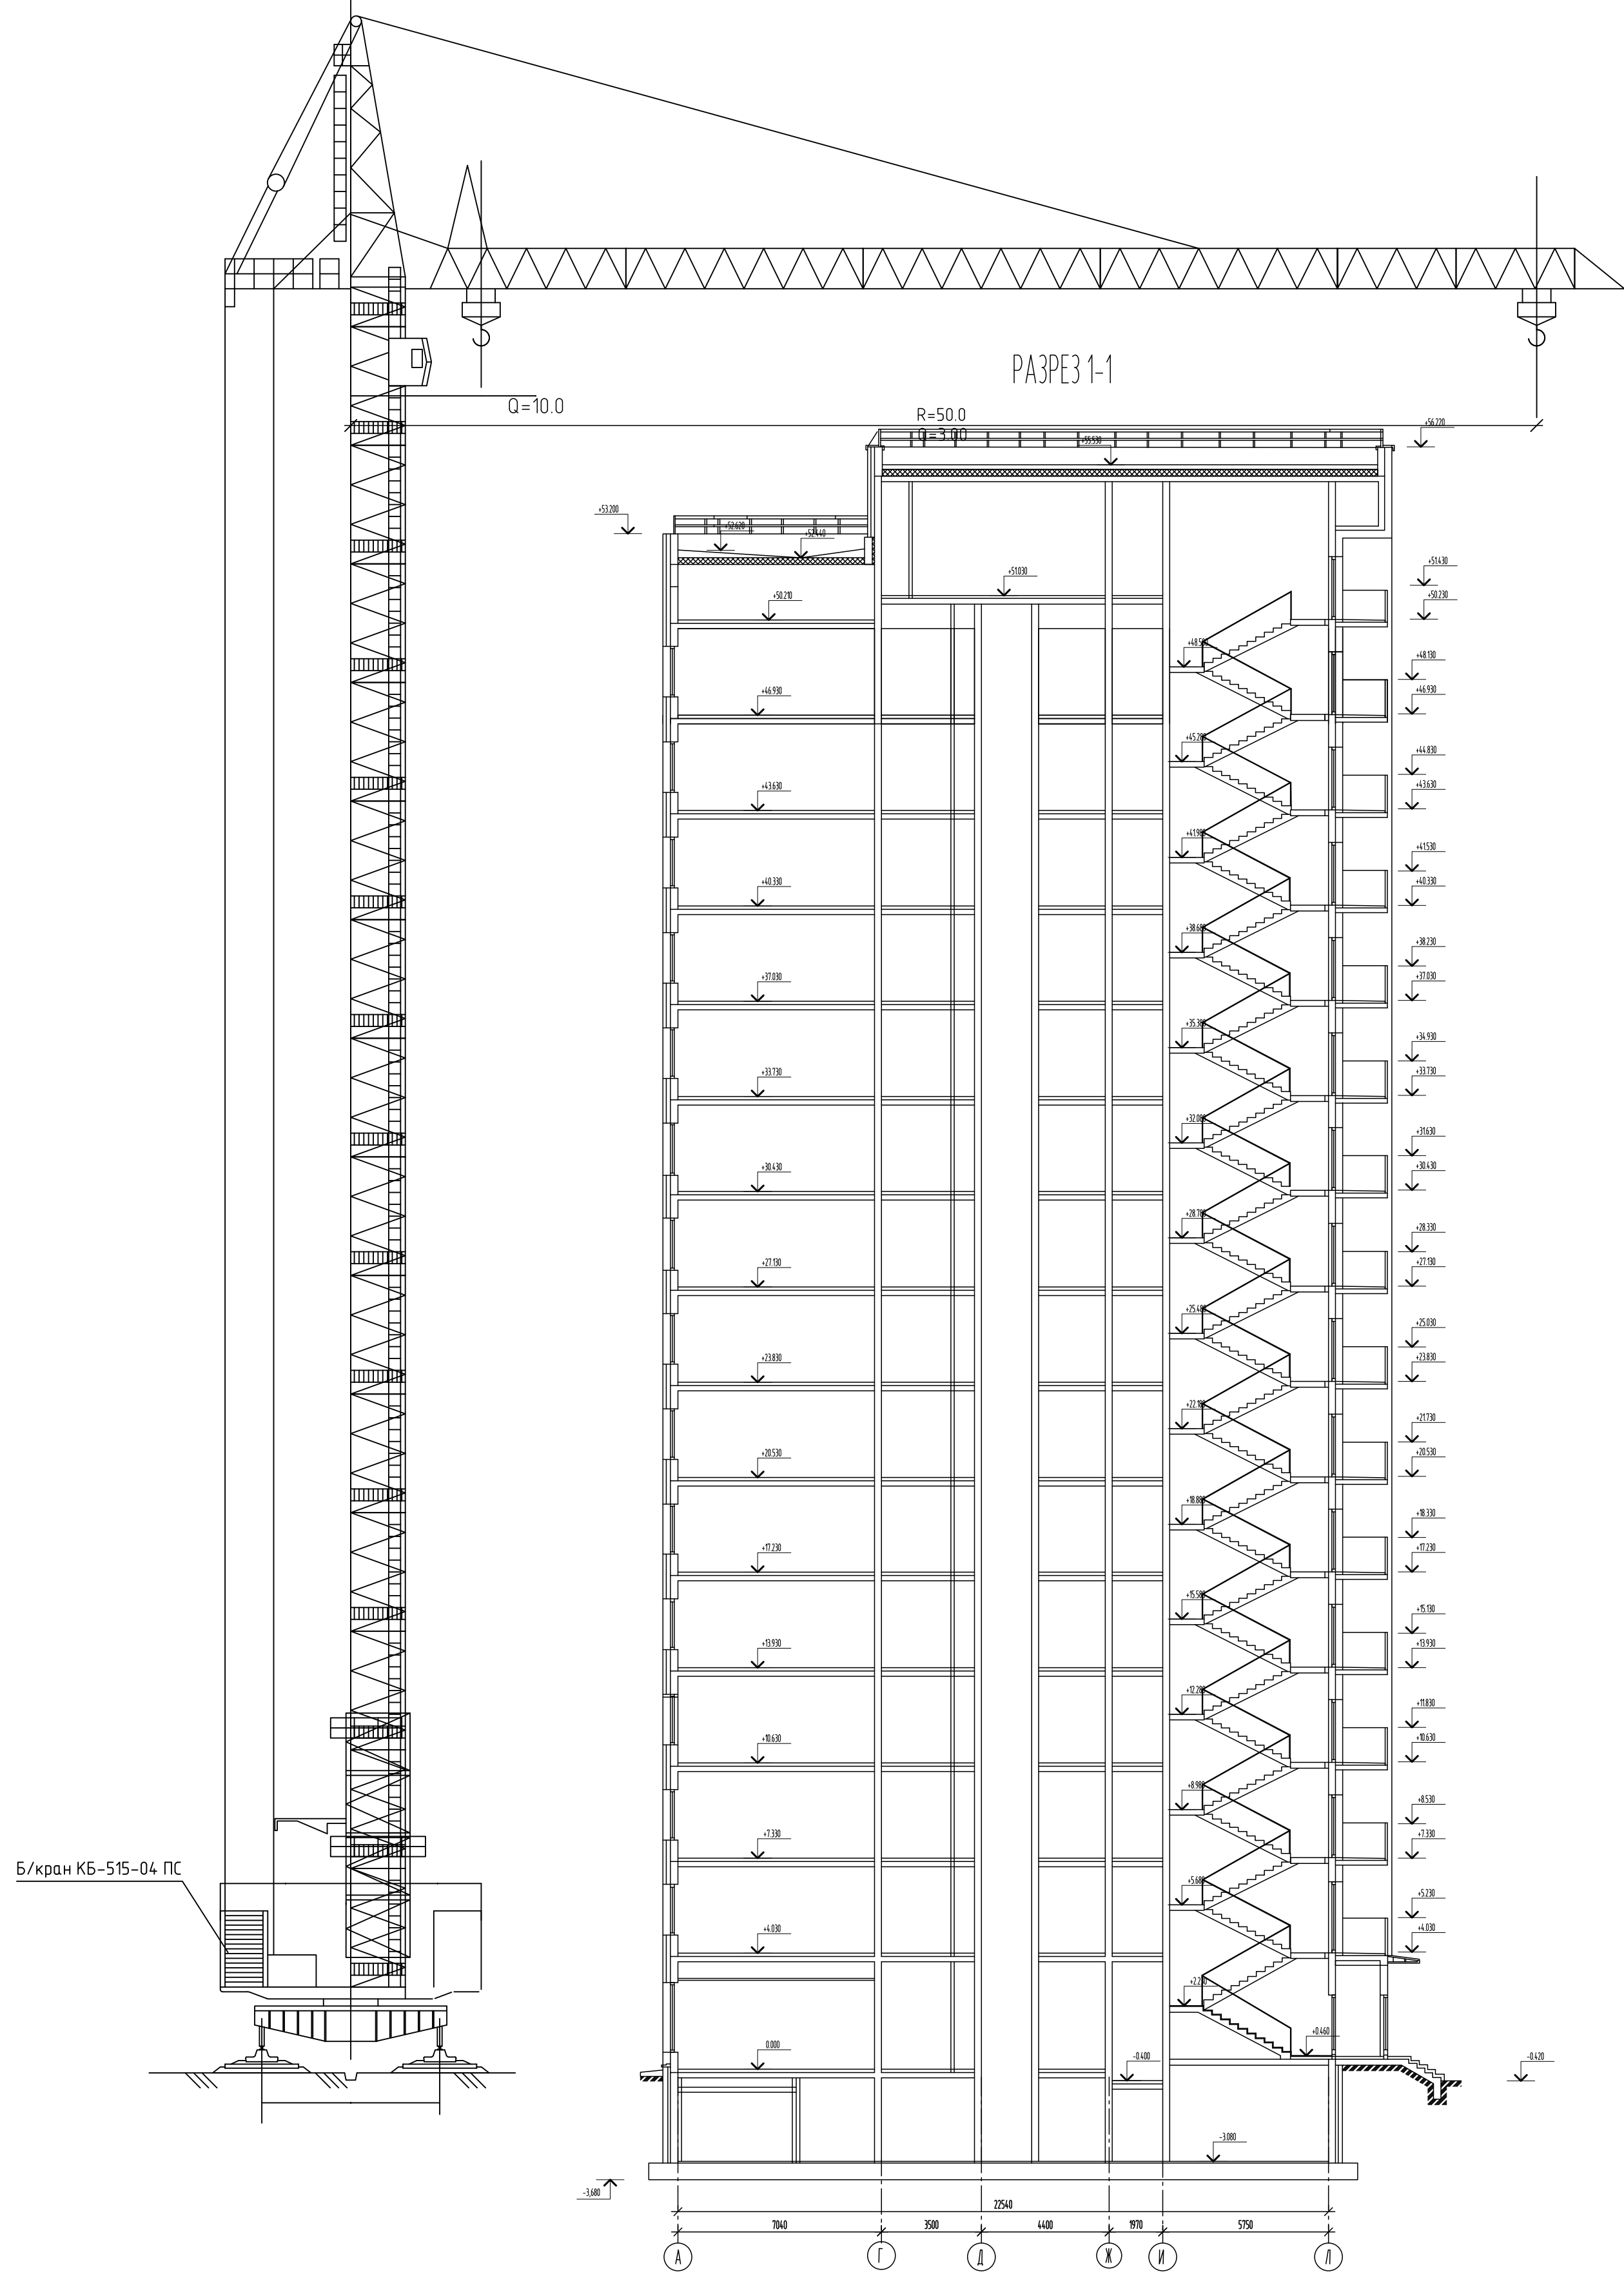

				КП 08.02.01 ПД-31					
				ОРГАНИЗАЦИОННО-ТЕХНОЛОГИЧЕСКАЯ ЧАСТЬ					
ДОЛЖНОСТЬ	ФИМИИ	ПОДПИСЬ	ДАТА				СТАДИ	ЛИСТ	ЛИСТОВ
				16-ТИ ЭТАЖНЫЙ МОНОЛИТНЫЙ ЖИЛОЙ ДОМ			У	1	5
ВЫПОЛНИЛ	ГЛАЗОВА МА			СПРОЕКТНО-ТЕХНОЛОГИЧЕСКАЯ ПРОЕКЦИЯ КР№ 16-56 МЭТУ; (технико-экономические показатели, 3-х этажное здание с жилыми помещениями, лоджиями и санузлами помещений); Те характеристики кр№ 16-55; Тех характеристики таблицы № 16-72А.			КАС №7		
РАБОТОУП.	ЖИЧЕНОВА ИВ								
КОМПЬЮТ.	САФОНОВА ОМ								
ПРОИОЛ	ЖИЧЕНОВА ИВ								