ФАСАД 1-9

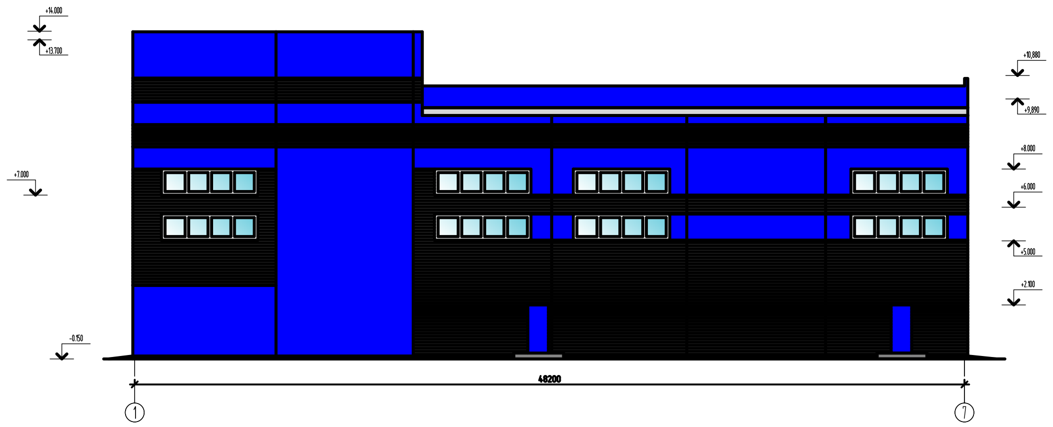

РАЗРЕЗ 1-1

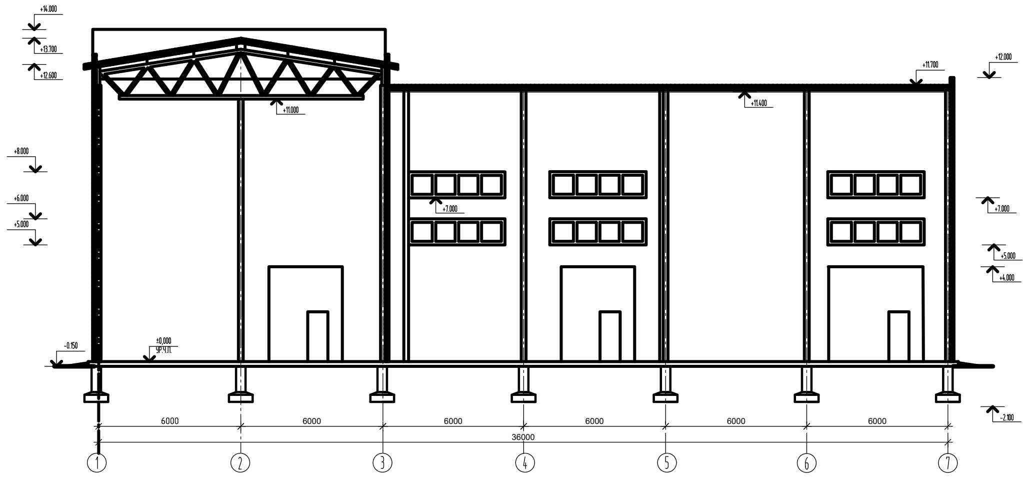

ПЛАН ФУНДАМЕНТА

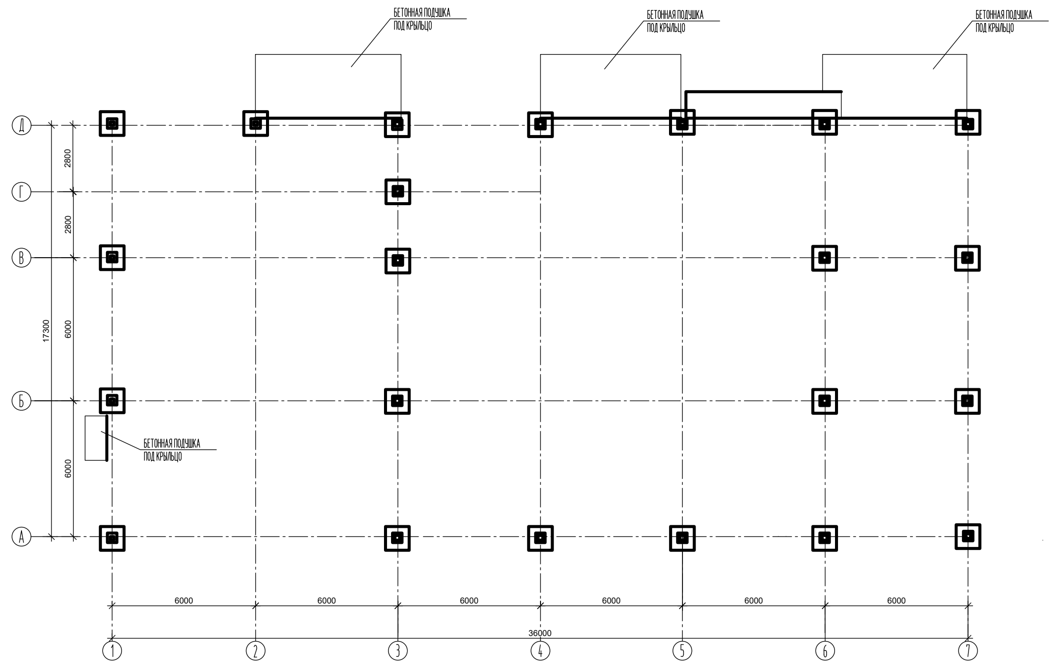
БЕТОННАЯ ПОДУШКА ПОД КРЫЛЬЦО
БЕТОННАЯ ПОДУШКА ПОД КРЫЛЬЦО
БЕТОННАЯ ПОДУШКА ПОД КРЫЛЬЦО
БЕТОННАЯ ПОДУШКА ПОД КРЫЛЬЦО
Д
Г
В
Б
А
2800
2800
6000
6000
17300
6000
6000
6000
6000
6000
6000
36000
1
2
3
4
5
6
7

ЭКСПЛИКАЦИЯ ПОМЕЩЕНИЙ		
п/п.п	НАИМЕНОВАНИЕ ПОМЕЩЕНИЯ	ПЛОЩАДЬ М^2
1	Склад	215.55
2	Склад	185.6
3	Комната отдыха	11.74
4	С/у	5.12
5	Склад	52.75
6	Тамбур	18.76
2	Душевая	18.33
3	С/у	16.77
9	Склад	147.92
10	Комната управляющего	9.04
11	Бойлерная	9.04
12	Электрощитовая	40.63
13	Торговый зал	103.93
ИТОГО		2649.83

СОВМЕЩЕННЫЙ ПЛАН ПОКРЫТИЯ И КРОВЛИ

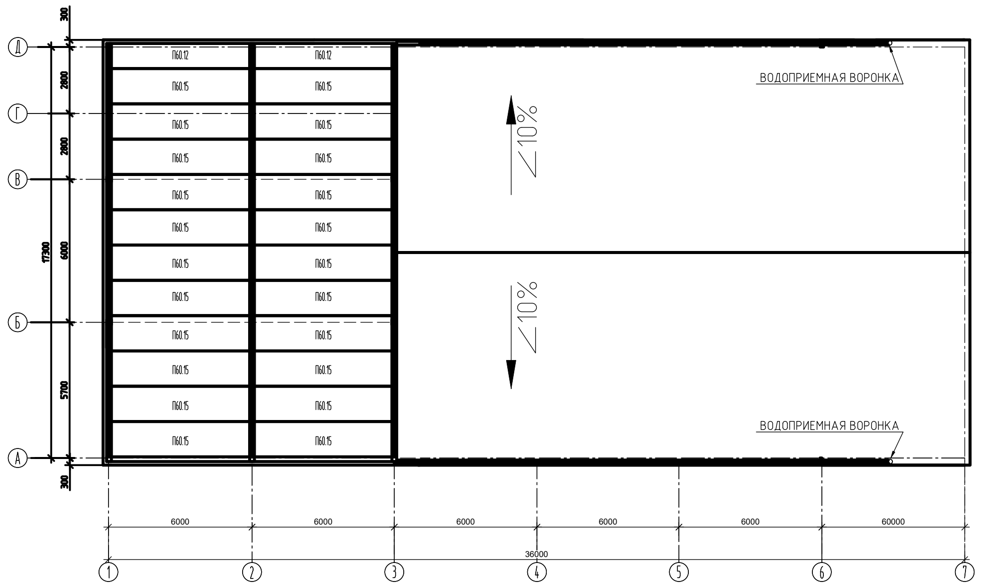

ПЛАН ЭТАЖА

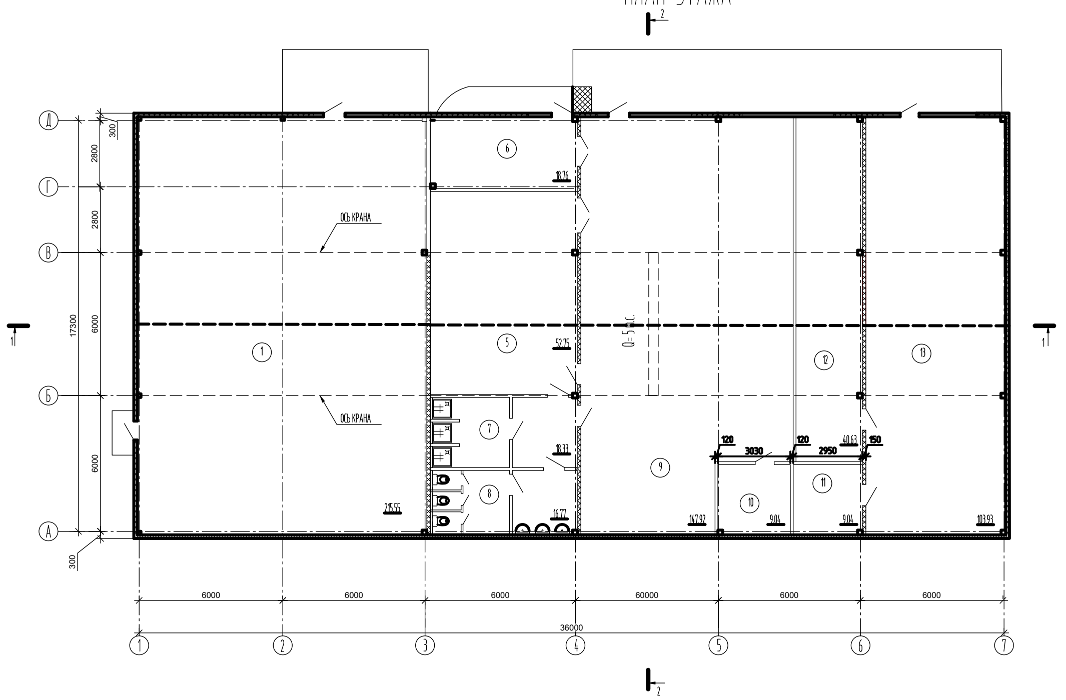

РАЗРЕЗ 2-2

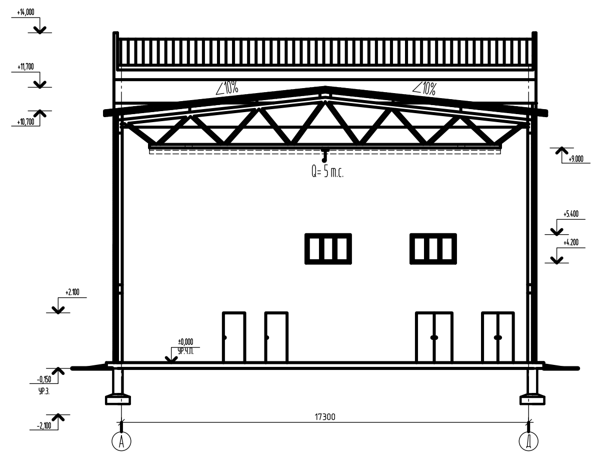

СПЕЦИФИКАЦИЯ МЕТАЛЛОКОНСТРУКЦИЙ		
НАИМЕНОВАНИЕ	РАЗМЕРЫ	КОЛ-ВО
1	300 х 200 х 17250	7

СПЕЦИФИКАЦИЯ КОЛОНН		
НАИМЕНОВАНИЕ	РАЗМЕРЫ	КОЛ-ВО
1ФК84-1	200 Х 200 Х 11500	22

СПЕЦИФИКАЦИЯ ПЛИТ ПОКРЫТИЙ		
НАИМЕНОВАНИЕ	РАЗМЕРЫ	КОЛ-ВО
ПБ 60.12	5980 Х 1190 Х 400	7
ПБ 60.15	5980 Х 1490 Х 400	77

СПЕЦИФИКАЦИЯ СБОРНОГО ФУНДАМЕНТА		
НАИМЕНОВАНИЕ	РАЗМЕРЫ	КОЛ-ВО
1Ф-9-9-1	1000 х 1000 х 1000	22

ДОЛЖНОСТЬ	ФАМИЛИЯ	ПОДПИСЬ	ДАТА
ВЫПОЛНИЛ.	ГЛАЗКОВА М.А.		
КОНСУЛЬТ.	ГОРЯЕВА Г.Н.		
ПРИНЯЛ	ГОРЯЕВА Г.Н.		

КР 08.02.01 ПД-31

АРХИТЕКТУРНАЯ И КОНСТРУКТИВНАЯ ЧАСТЬ

СКЛАД ИЗ МЕТАЛЛОПРОФИЛЯ

СТАДИЯ	ЛИСТ	ЛИСТОВ
У	1	1

ПЛАН ПОМЕЩЕНИЯ; ФАСАД 1-8; РАЗРЕЗ 1-1, 2-2; СОВМЕЩЕННЫЙ ПЛАН ПОКРЫТИЯ И КРОВЛИ; ПЛАН ФУНДАМЕНТА; СПЕЦИФИКАЦИИ ОКОН И ДВЕРЕЙ, КОЛОНН, СБОРНОГО ФУНДАМЕНТА МЕТАЛЛОКОНСТРУКЦИЙ, ЭКСПЛИКАЦИЯ ПОМЕЩЕНИЙ

КАС №7

Формат А0